

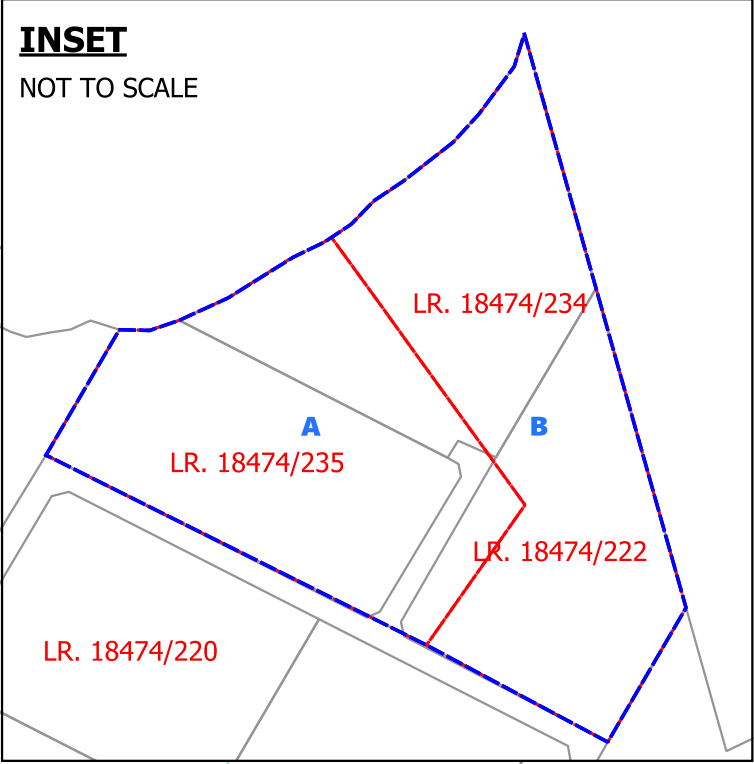


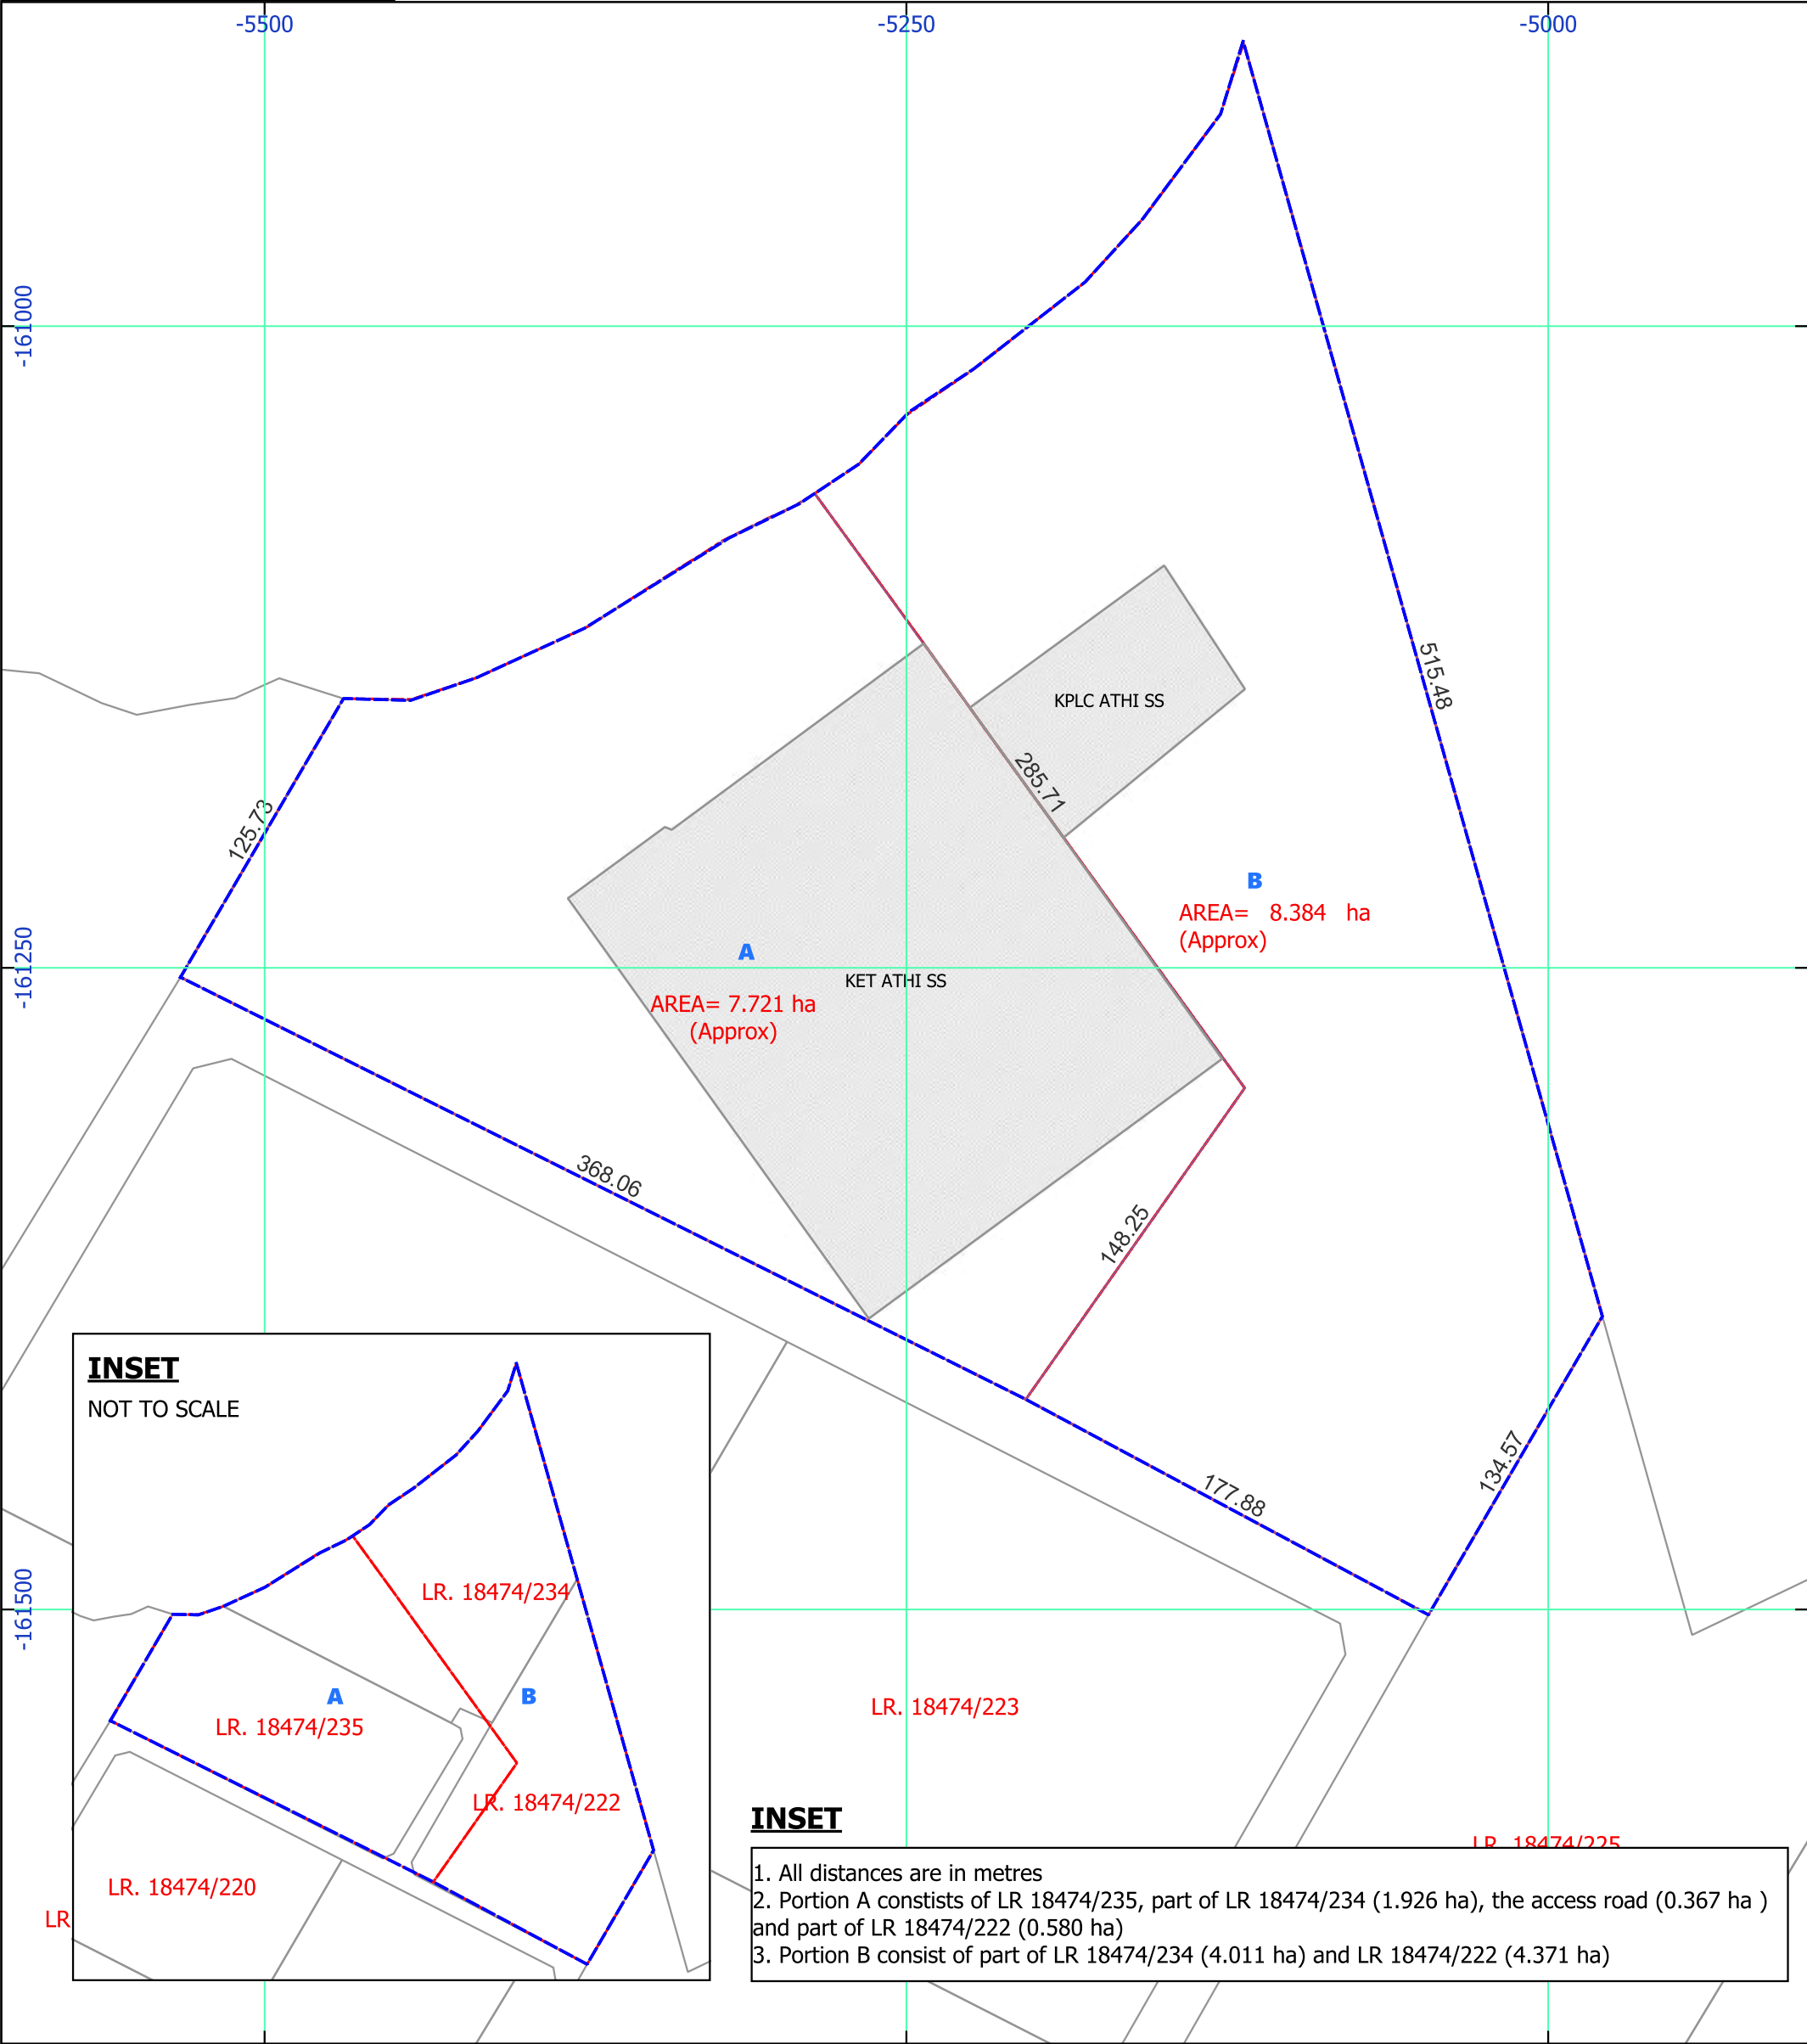

- INSET**
1. All distances are in metres
 2. Portion A consists of LR 18474/235, part of LR 18474/234 (1.926 ha), the access road (0.367 ha) and part of LR 18474/222 (0.580 ha)
 3. Portion B consist of part of LR 18474/234 (4.011 ha) and LR 18474/222 (4.371 ha)

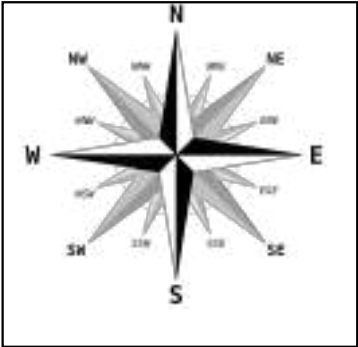

Legend



Existing Substations

Proposed Subdivisions

Proposed Amalgamation

COORDINATES REFERRED TO EQUATOR & 37° EAST


SCALE; 1:2,500

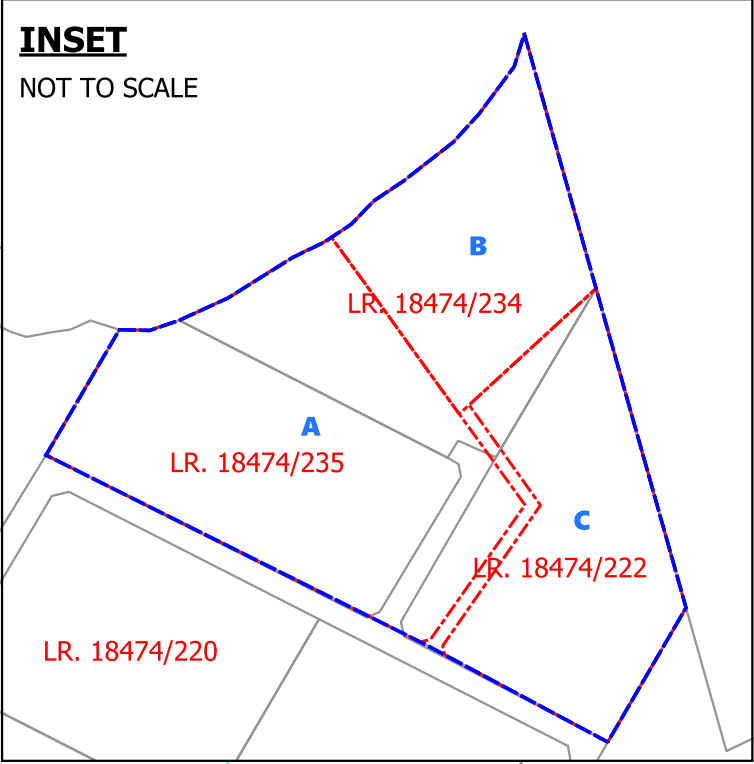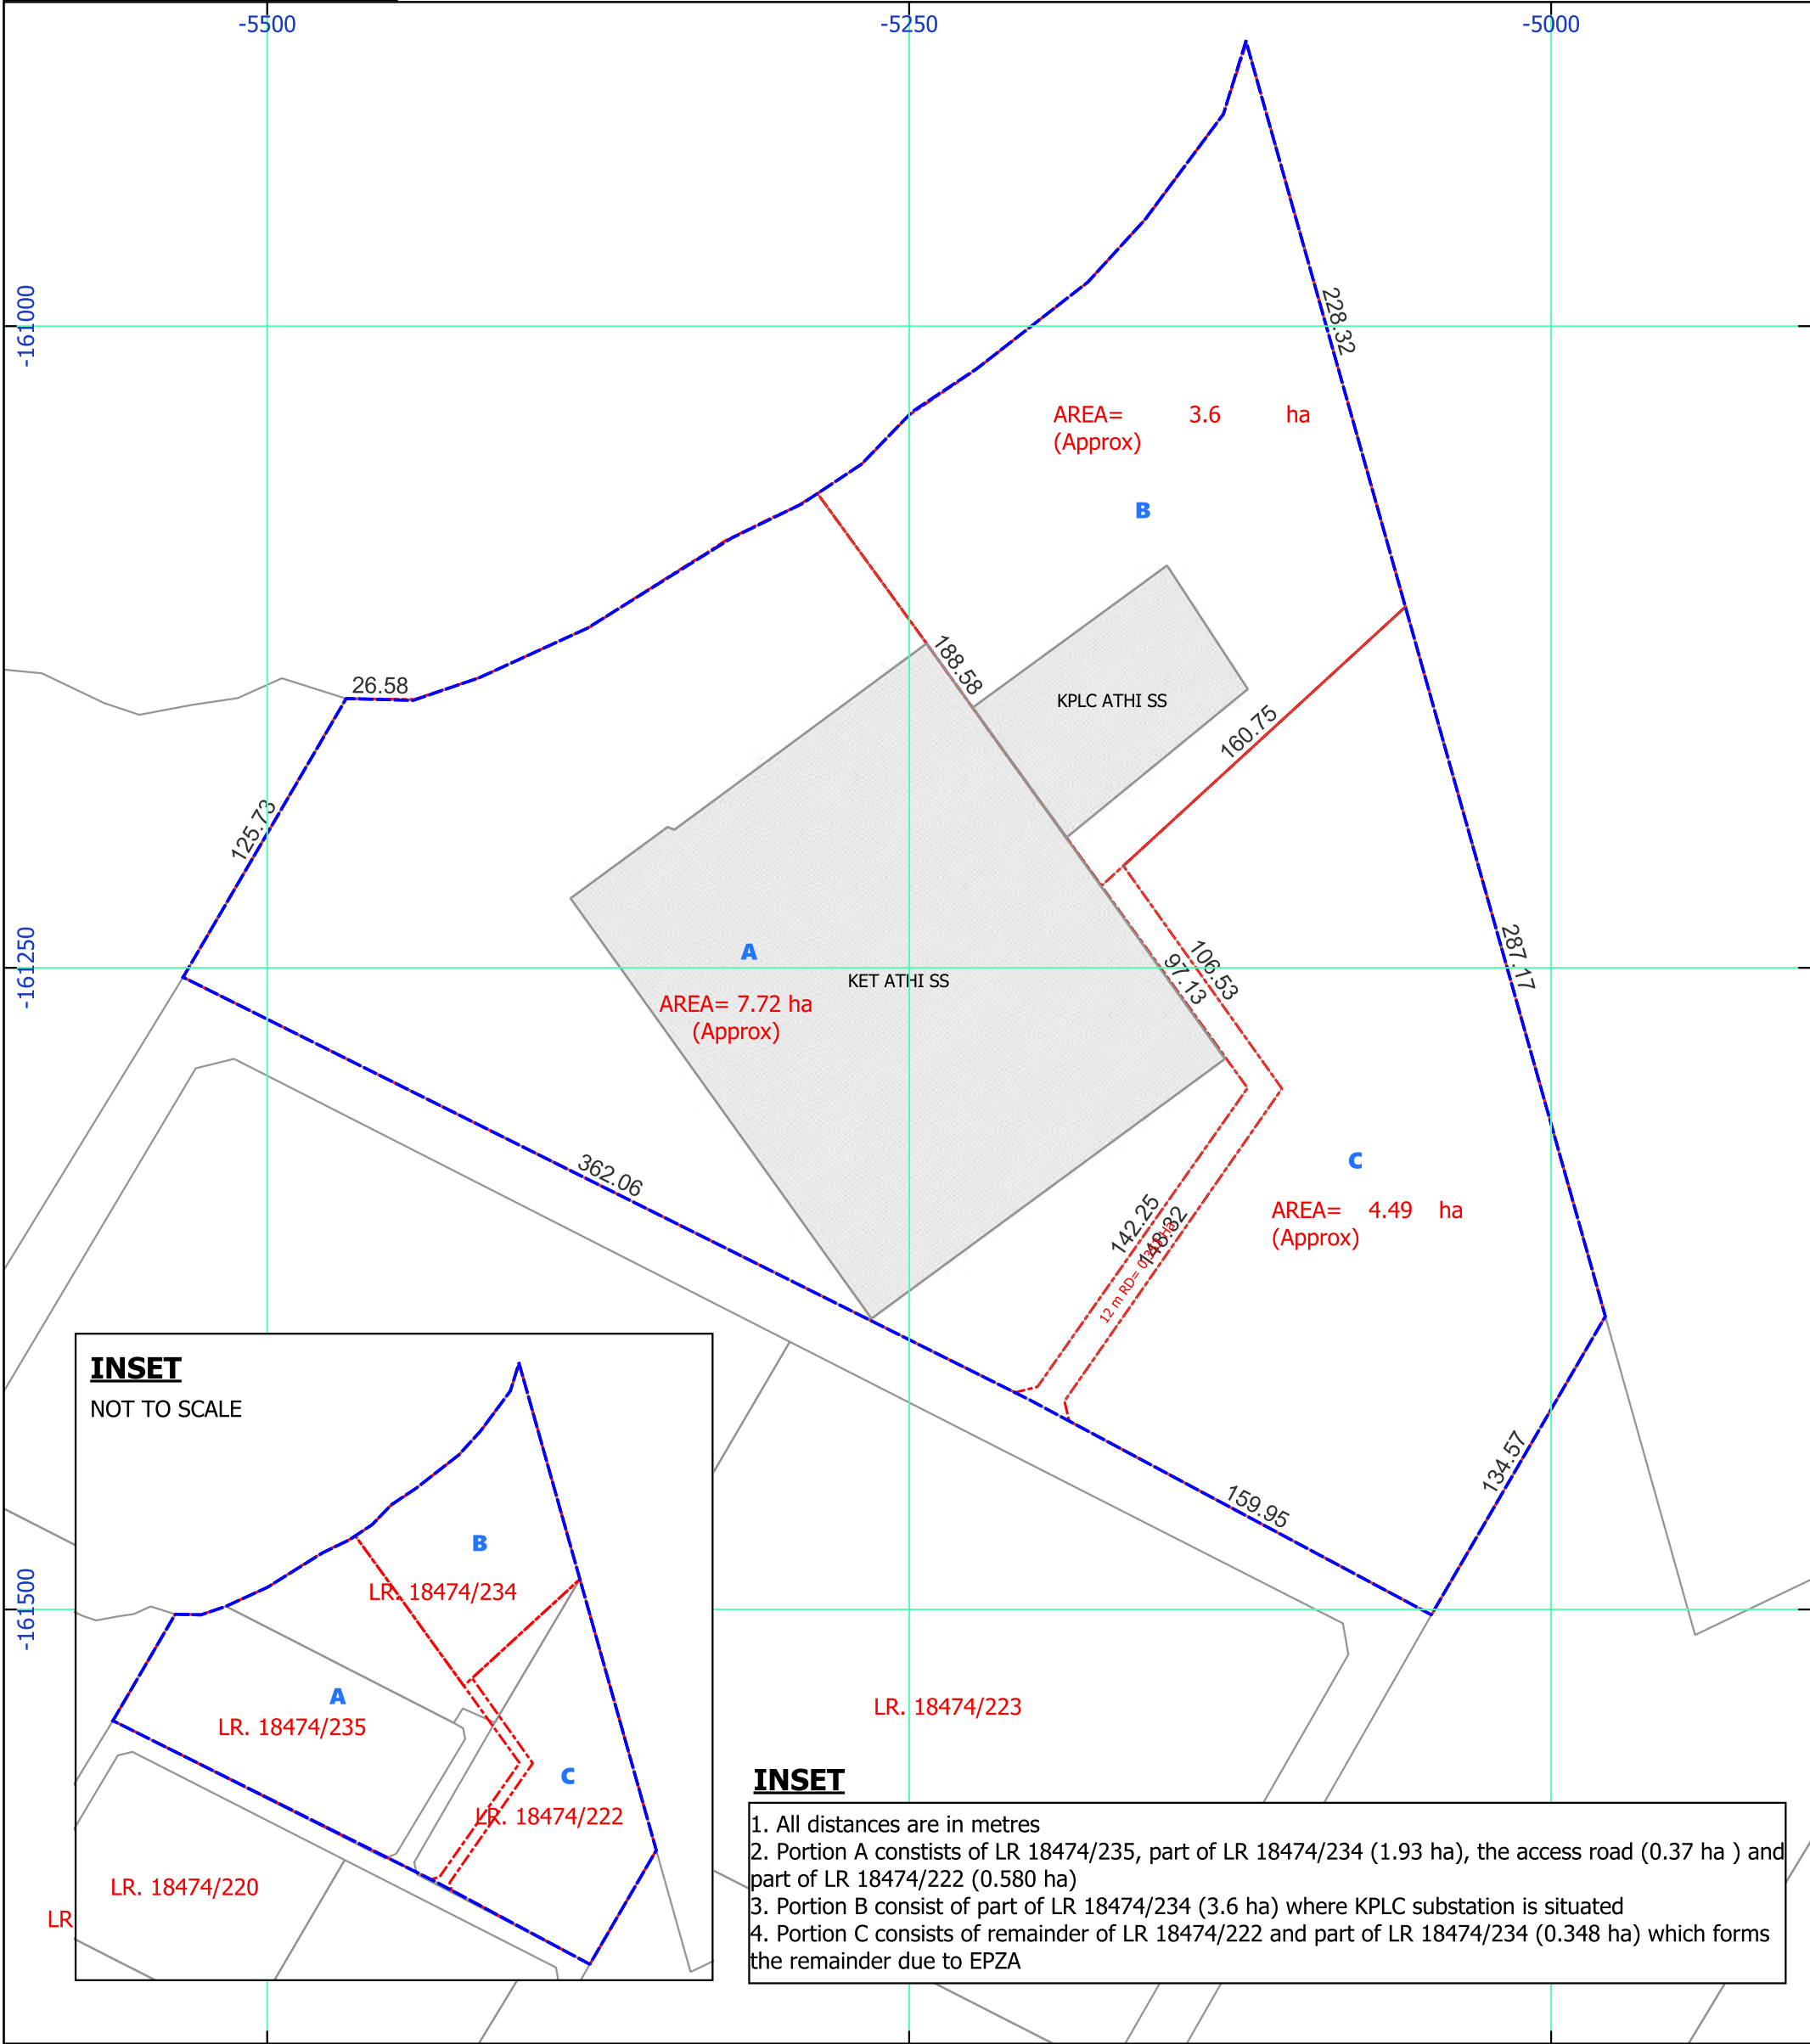

- INSET**
1. All distances are in metres
 2. Portion A consists of LR 18474/235, part of LR 18474/234 (1.93 ha), the access road (0.37 ha) and part of LR 18474/222 (0.580 ha)
 3. Portion B consist of part of LR 18474/234 (3.6 ha) where KPLC substation is situated
 4. Portion C consists of remainder of LR 18474/222 and part of LR 18474/234 (0.348 ha) which forms the remainder due to EPZA



KETRACO
Kenya Electricity Transmission Co. Ltd.
"Building a World Class National Grid"

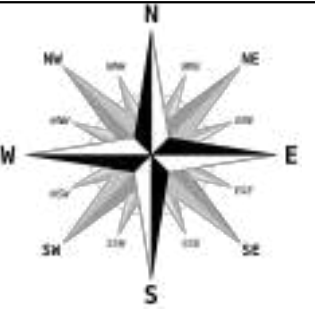

Legend


- Existing Substations
- Proposed Subdivisions
- Proposed Amalgamation

COORDINATES REFERRED TO EQUATOR & 37° EAST


SCALE; 1:2,500

DATE: 17-03-2023



OPTION B: REGRANT OF ACCESS ROAD & AMALGAMATION OF LR
18474/222,/234,/235 & PARTITION INTO THREE PORTIONS

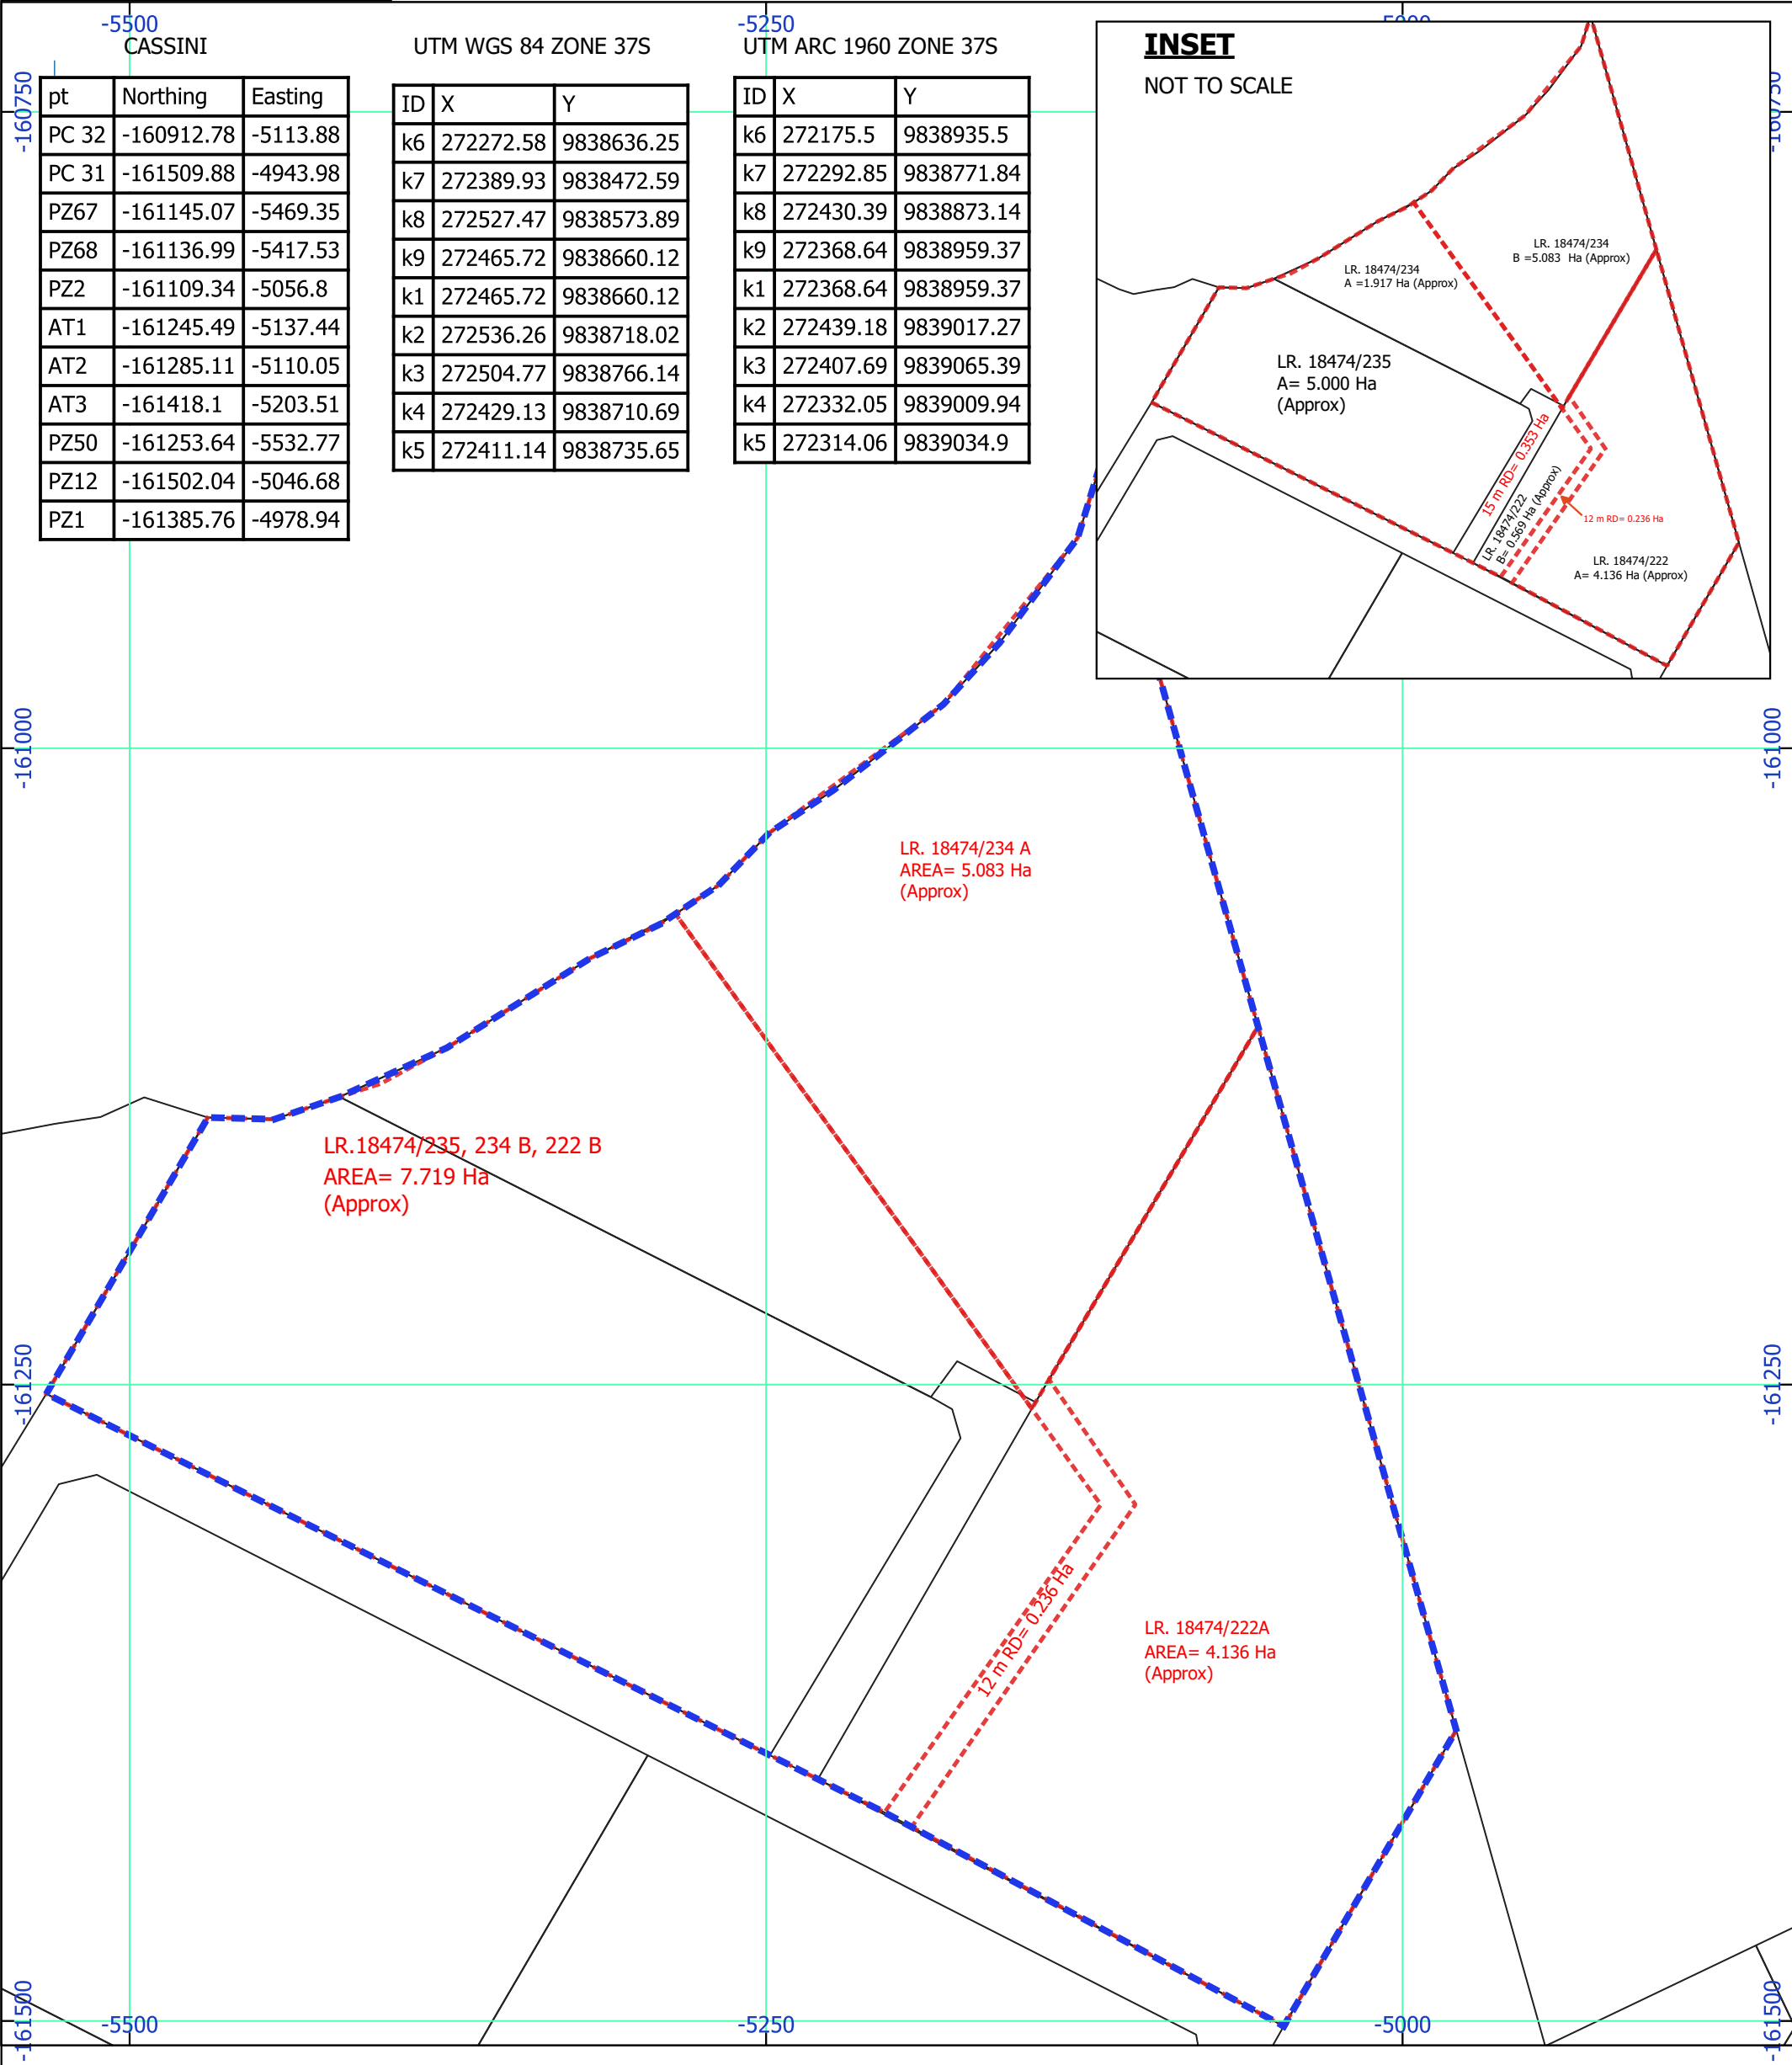

BIRDS MIGRATION INTO KENYA

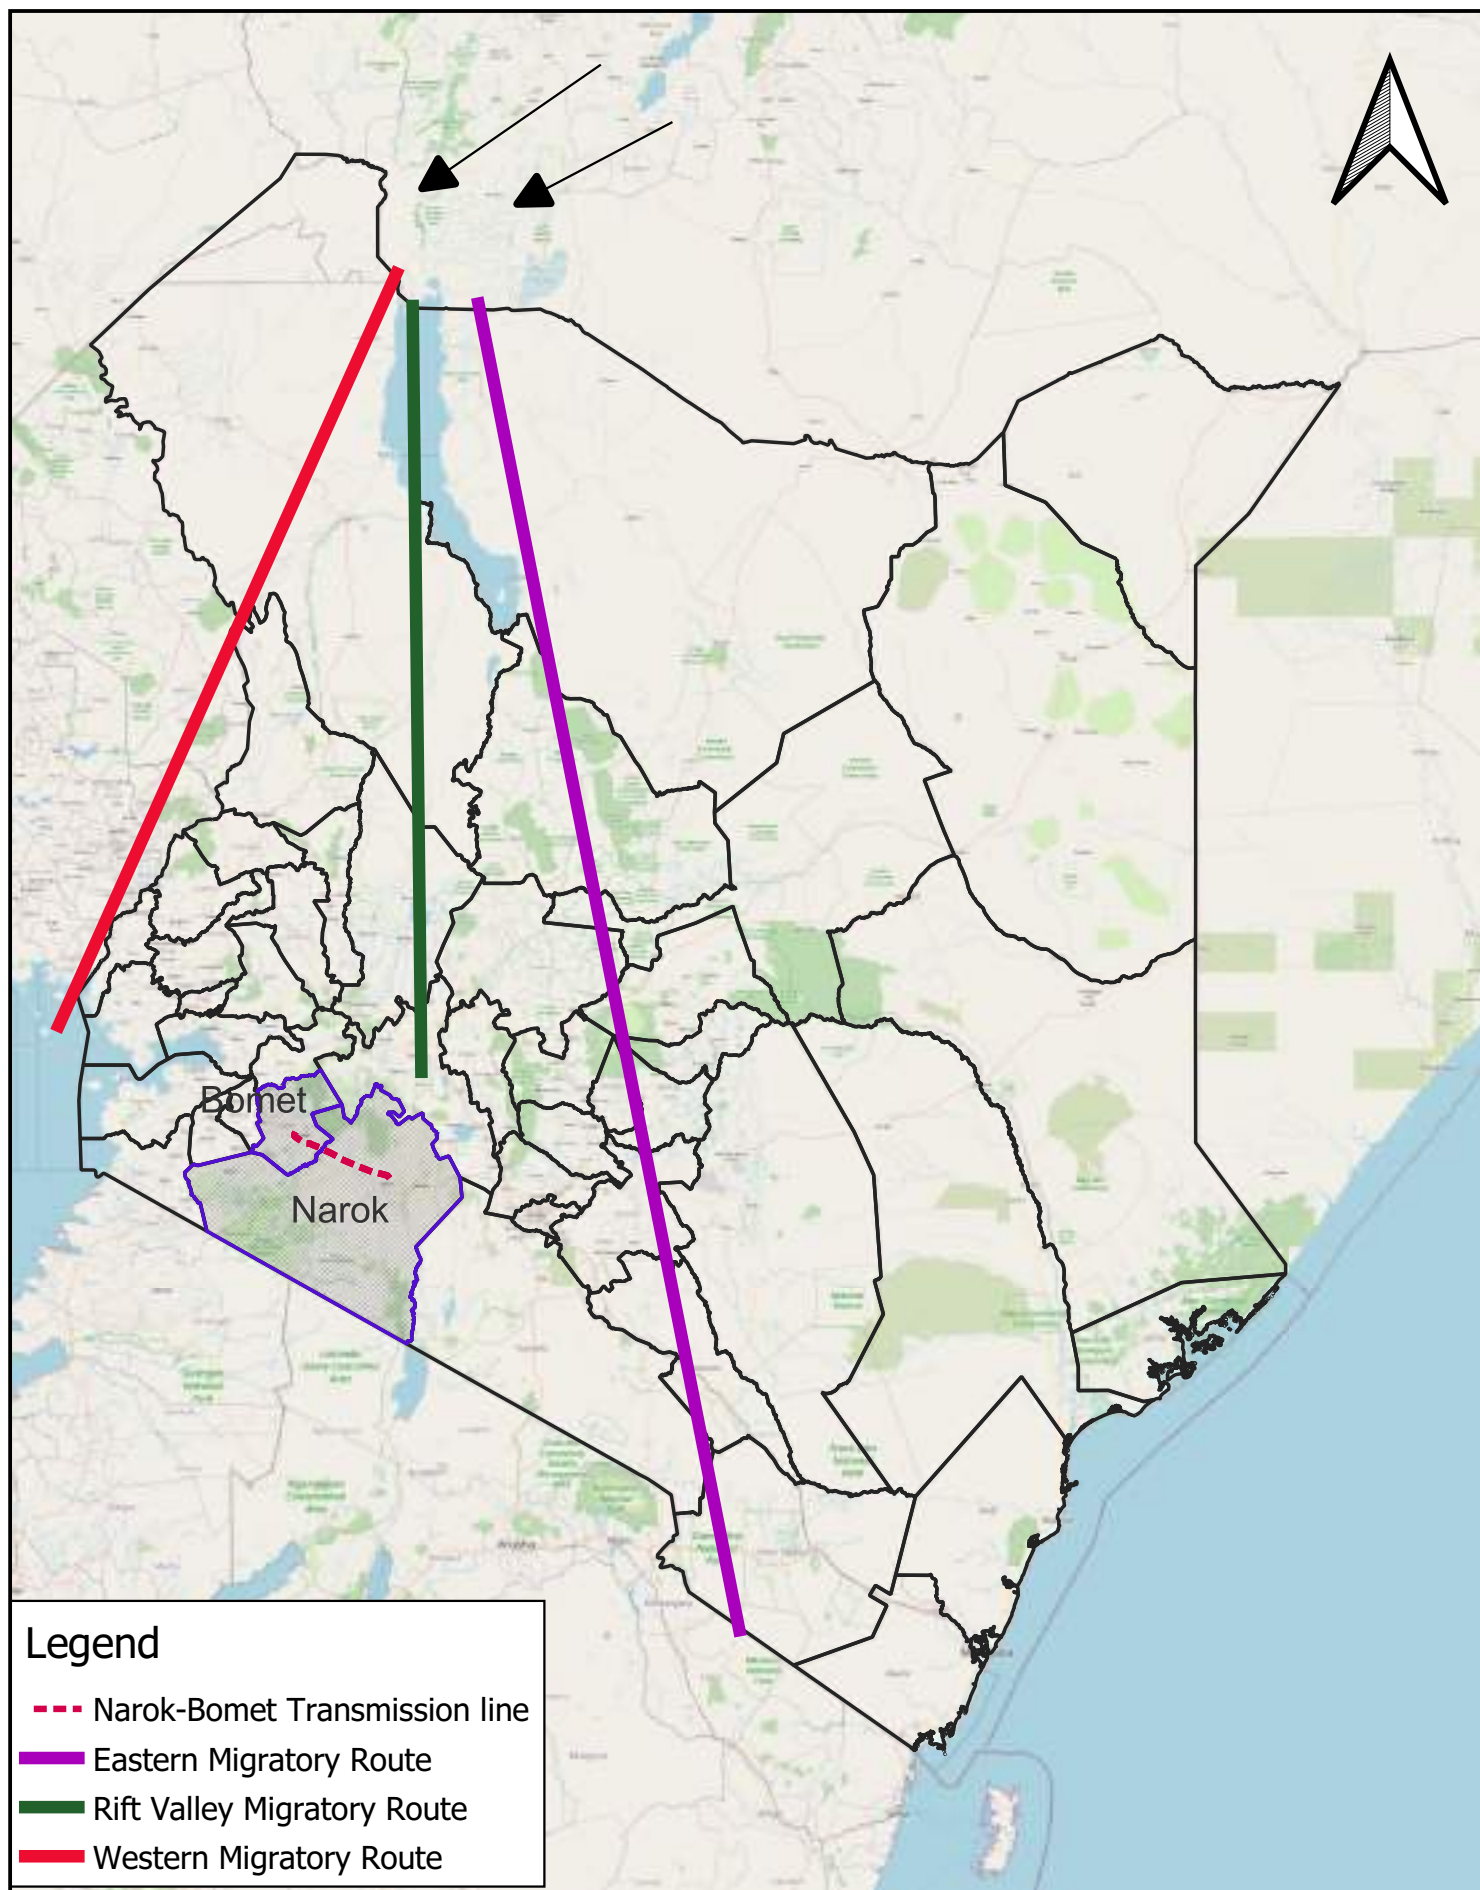

Subdivision of LR. No 13963 (South Ngariama Settlement Scheme-Kirinvaga County)

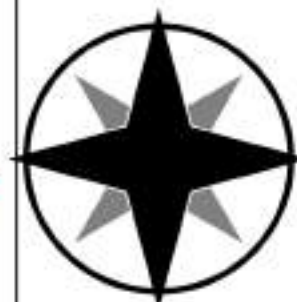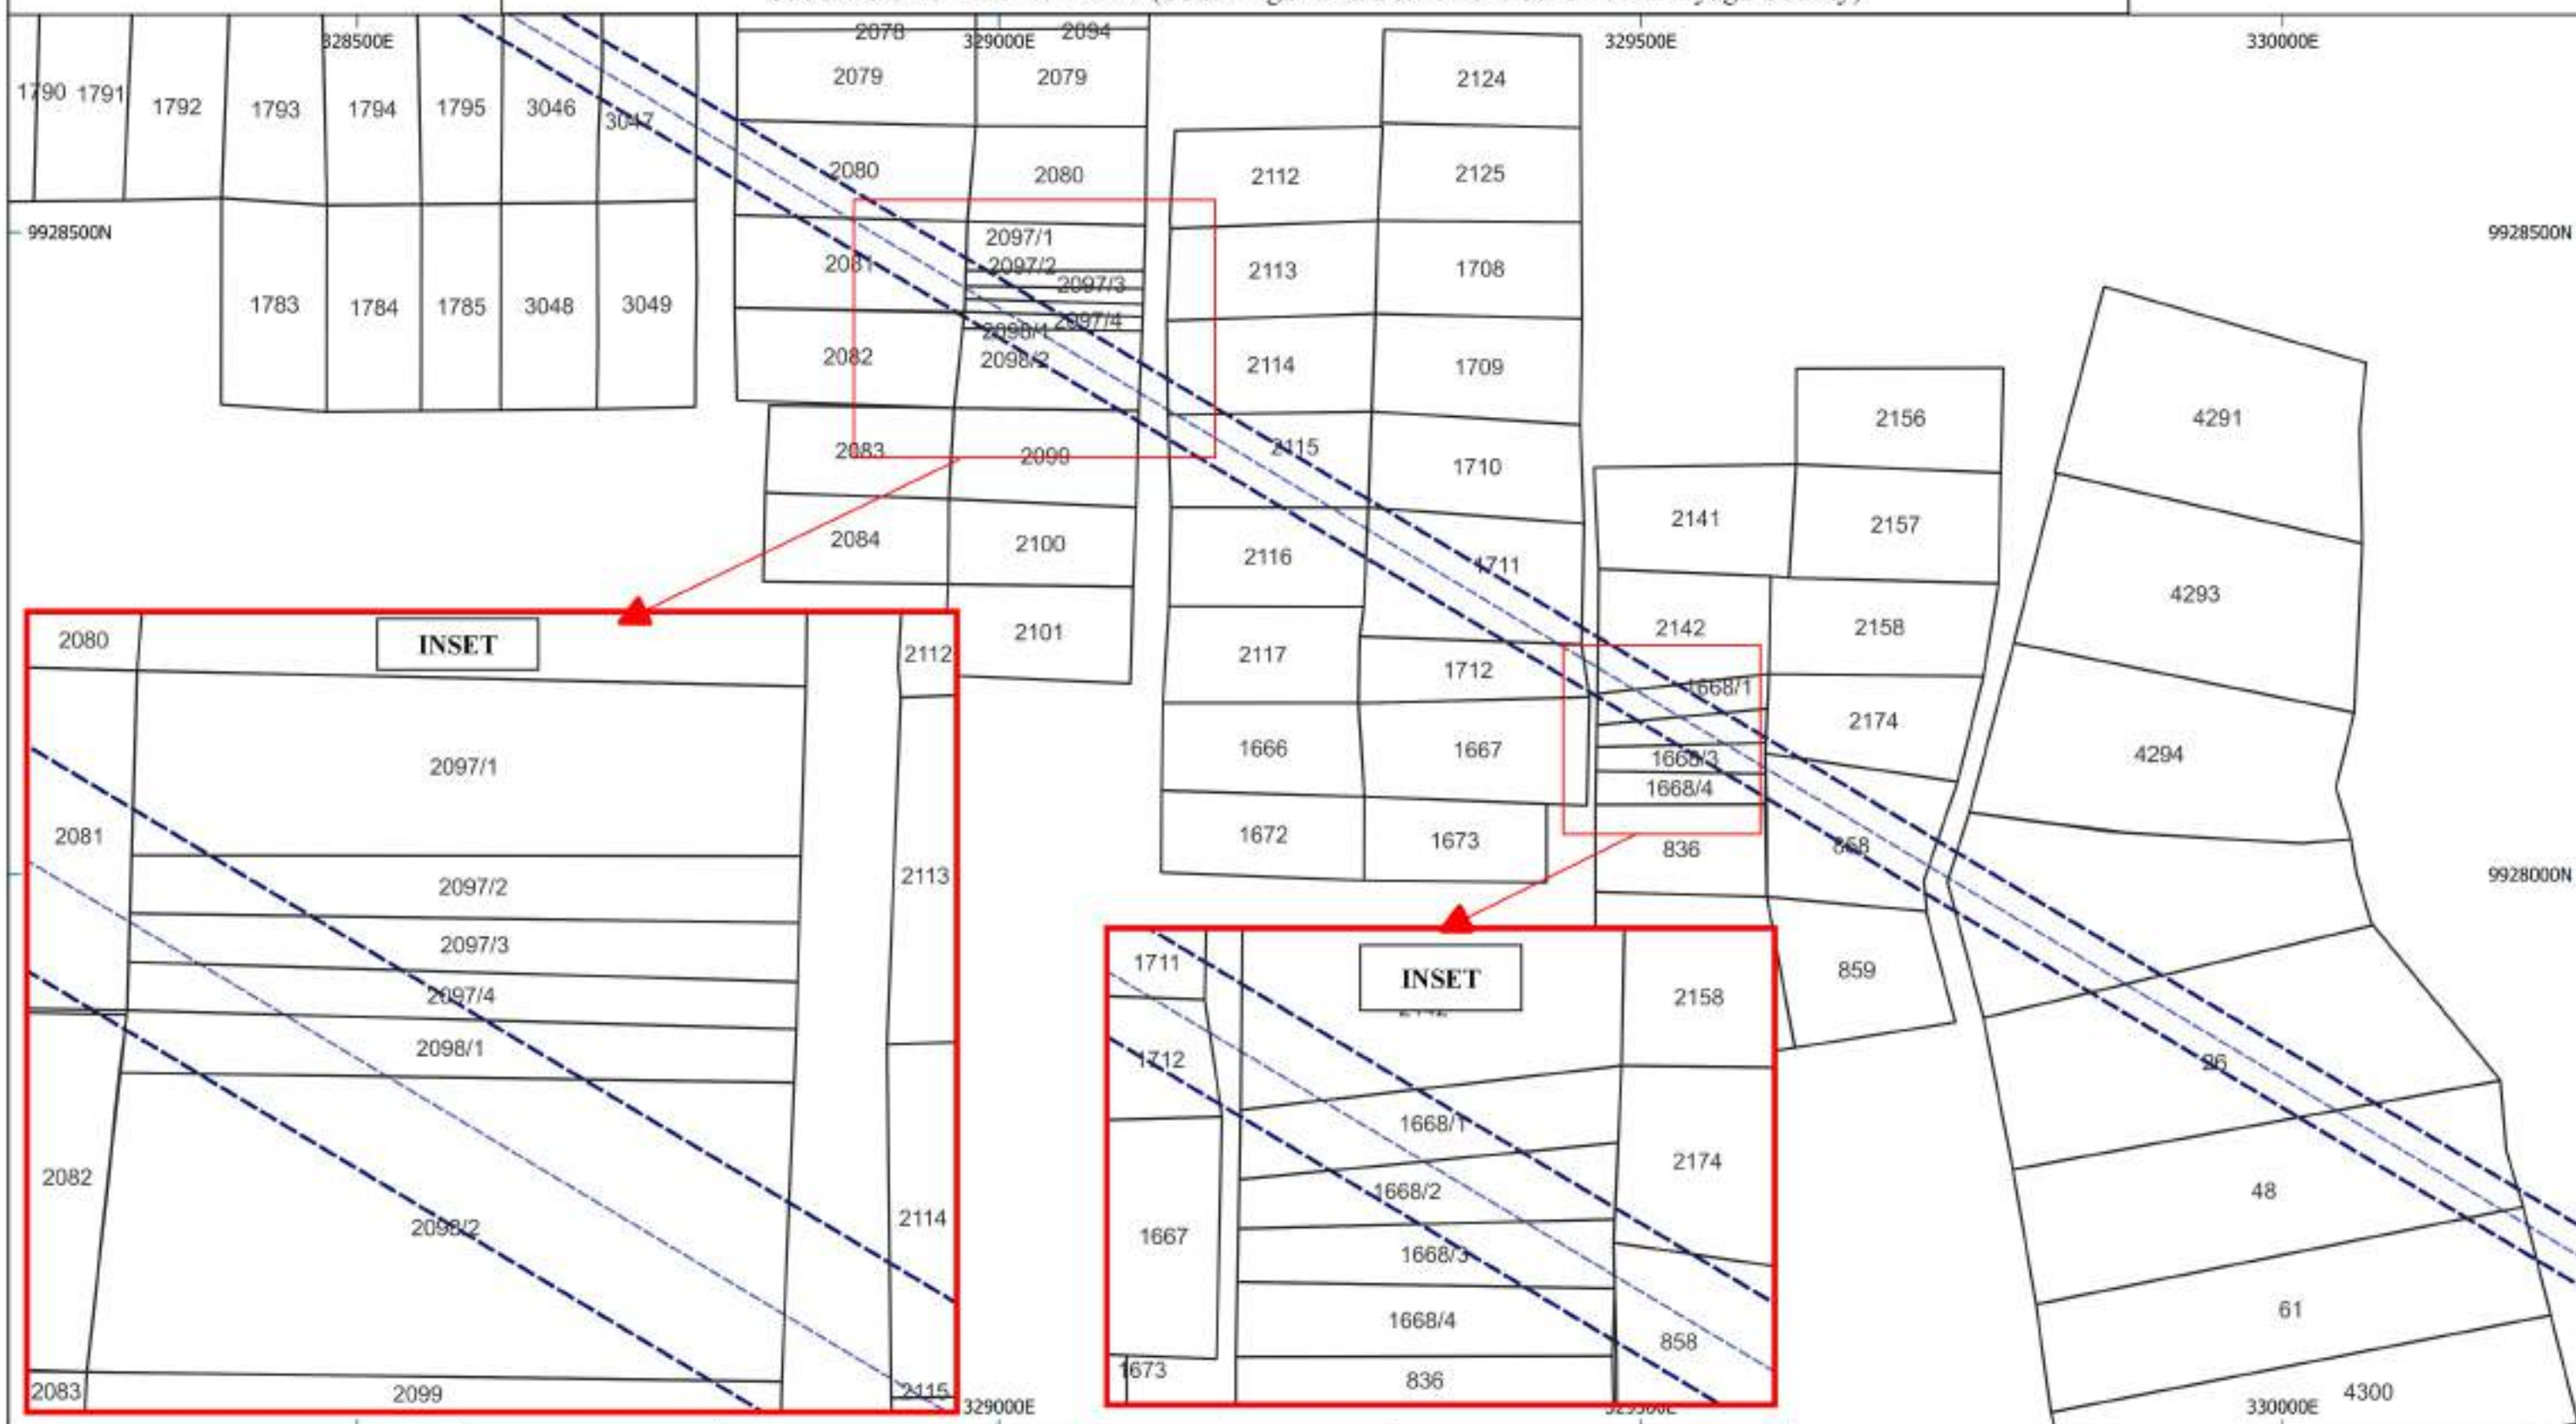

COORDINATE SYSTEM:

UTM Projection
Datum: Arc 1960
Zone 37S
Units: Metres
EPSG: 21037

This map is not conclusive on the precise position on any boundaries unless this has been fixed in accordance with Sec. 22 of Land Registration Act.

Surveyed and Drawn by:

1. Victor Oundo
2. Raphael Birisha.....
3. Justus Kilonzi.....

Approved by: Frederik O. Oduor

Manager -Survey, Mapping & GIS

Legend

--- Transmission Line
 □ Wayleave Corridor
 □ Parcels



COORDINATE SYSTEM:

UTM Projection
Datum: Arc 1960
Zone 37S
Units: Metres
EPSG: 21037

This map is not conclusive on the precise position on any boundaries unless this has been fixed in accordance with Sec. 22 of Land Registration Act.

Surveyed and Drawn by:

1. Victor Oundo
2. Raphael Birisha.....
3. Justus Kilonzi.....

Approved by: Frederik O. Oduor

Manager -Survey, Mapping & GIS

Legend

-  Transmission Line
-  Wayleave Corridor
-  Parcels




MALAA SUBSTATION LAND



LR 2670/13

COORDINATES

Station	Lat	Lon	Northing	Easting	Y	X
Riv3	-1.183824679	37.17158476	9869383.72	296454.5	-130799.65	18917.22
Riv4	-1.186273789	37.17018647	9869112.78	296299.04	-131070.45	18761.58
F3	-1.186332558	37.18579703	9869107.42	298036.62	-131077.06	20498.96
F4	-1.188957545	37.18480596	9868817.06	297926.5	-131367.31	20388.64
DM3	-1.186066907	37.21489762	9869138.9	301275.69	-131047.92	23737.72
DM4	-1.188393461	37.21390153	9868881.55	301164.98	-131305.17	23626.84
KPW3	-1.184982394	37.17814558	9869256.17	297184.86	-130927.71	19647.4
KPW4	-1.187501768	37.1768757	9868977.47	297043.7	-131206.28	19506.05
KPE3	-1.18504875	37.17851487	9869248.86	297225.97	-130935.05	19688.5
KPE4	-1.187569481	37.17724436	9868970.01	297084.74	-131213.77	19547.08
KT1	-1.186173944	37.17024352	9869123.83	296305.38	-131059.41	18767.93
KT2	-1.184097159	37.1731286	9869353.7	296626.37	-130829.79	19089.04
KT3	-1.186482861	37.17192609	9869089.79	296492.69	-131093.58	18955.19
1C14	-1.187400837	37.17692663	9868988.64	297049.36	-131195.12	19511.72
KT5	-1.18746855	37.1772953	9868981.18	297090.4	-131202.61	19552.75
KT6	-1.188854355	37.18484495	9868828.48	297930.83	-131355.9	20392.98
TR1	-1.186107931	37.1686749	9869131.01	296130.78	-131052.1	18593.35
TR2	-1.186335849	37.16985537	9869105.89	296262.19	-131077.31	18724.73
TR3	-1.18522343	37.16918538	9869228.86	296187.53	-130954.3	18650.17
TR4	-1.183622105	37.17152689	9869406.12	296448.05	-130777.25	18910.78
TR5	-1.184342836	37.17231016	9869326.47	296535.28	-130856.95	18997.95
TR6	-1.185625537	37.17455643	9869184.79	296785.41	-130998.8	19247.94
TR7	-1.186840121	37.17707737	9869050.66	297066.09	-131133.12	19528.5
TR8	-1.188058277	37.18022889	9868916.18	297416.97	-131267.84	19879.24
TR9	-1.188500286	37.18228471	9868867.45	297645.83	-131316.73	20108.04
TR11	-1.186810061	37.18582949	9869054.62	298040.27	-131129.86	20502.57
Boma	-1.186861368	37.18131726	9869048.62	297538.03	-131135.5	20000.38

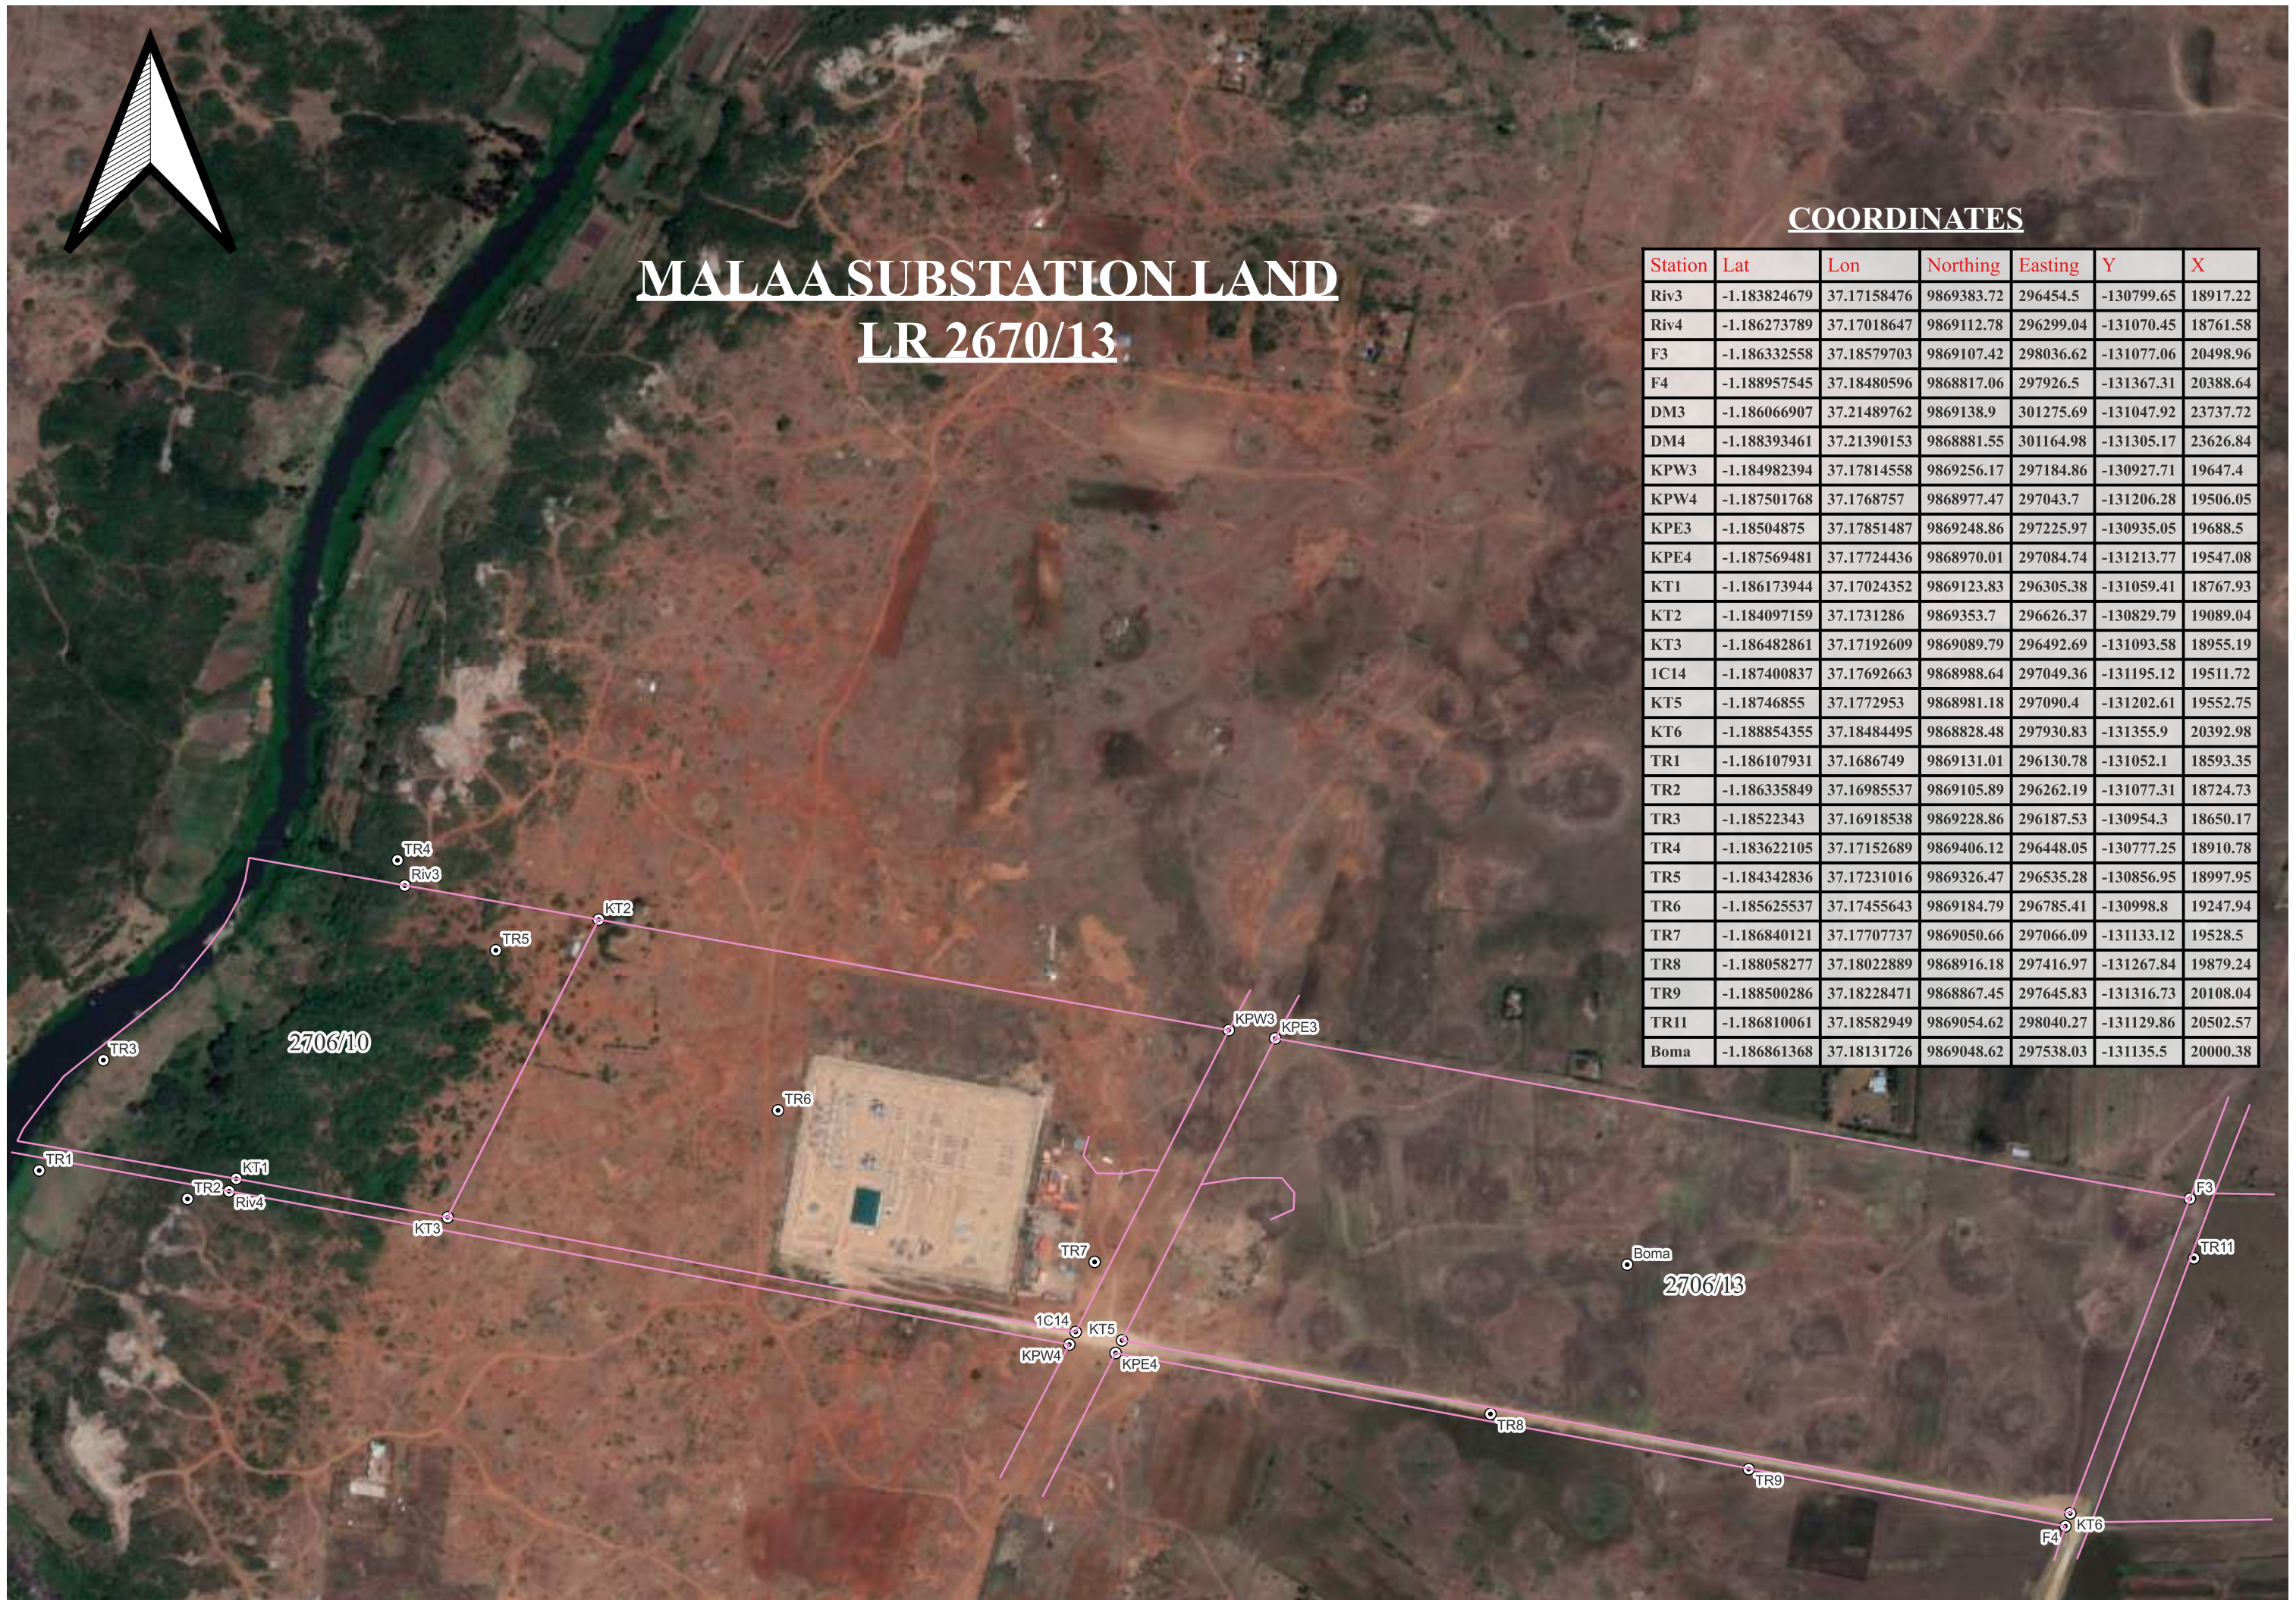

BILIQO BULESA COMMUNITY CONSERVANCY WILDLIFE OBSERVATION 2019

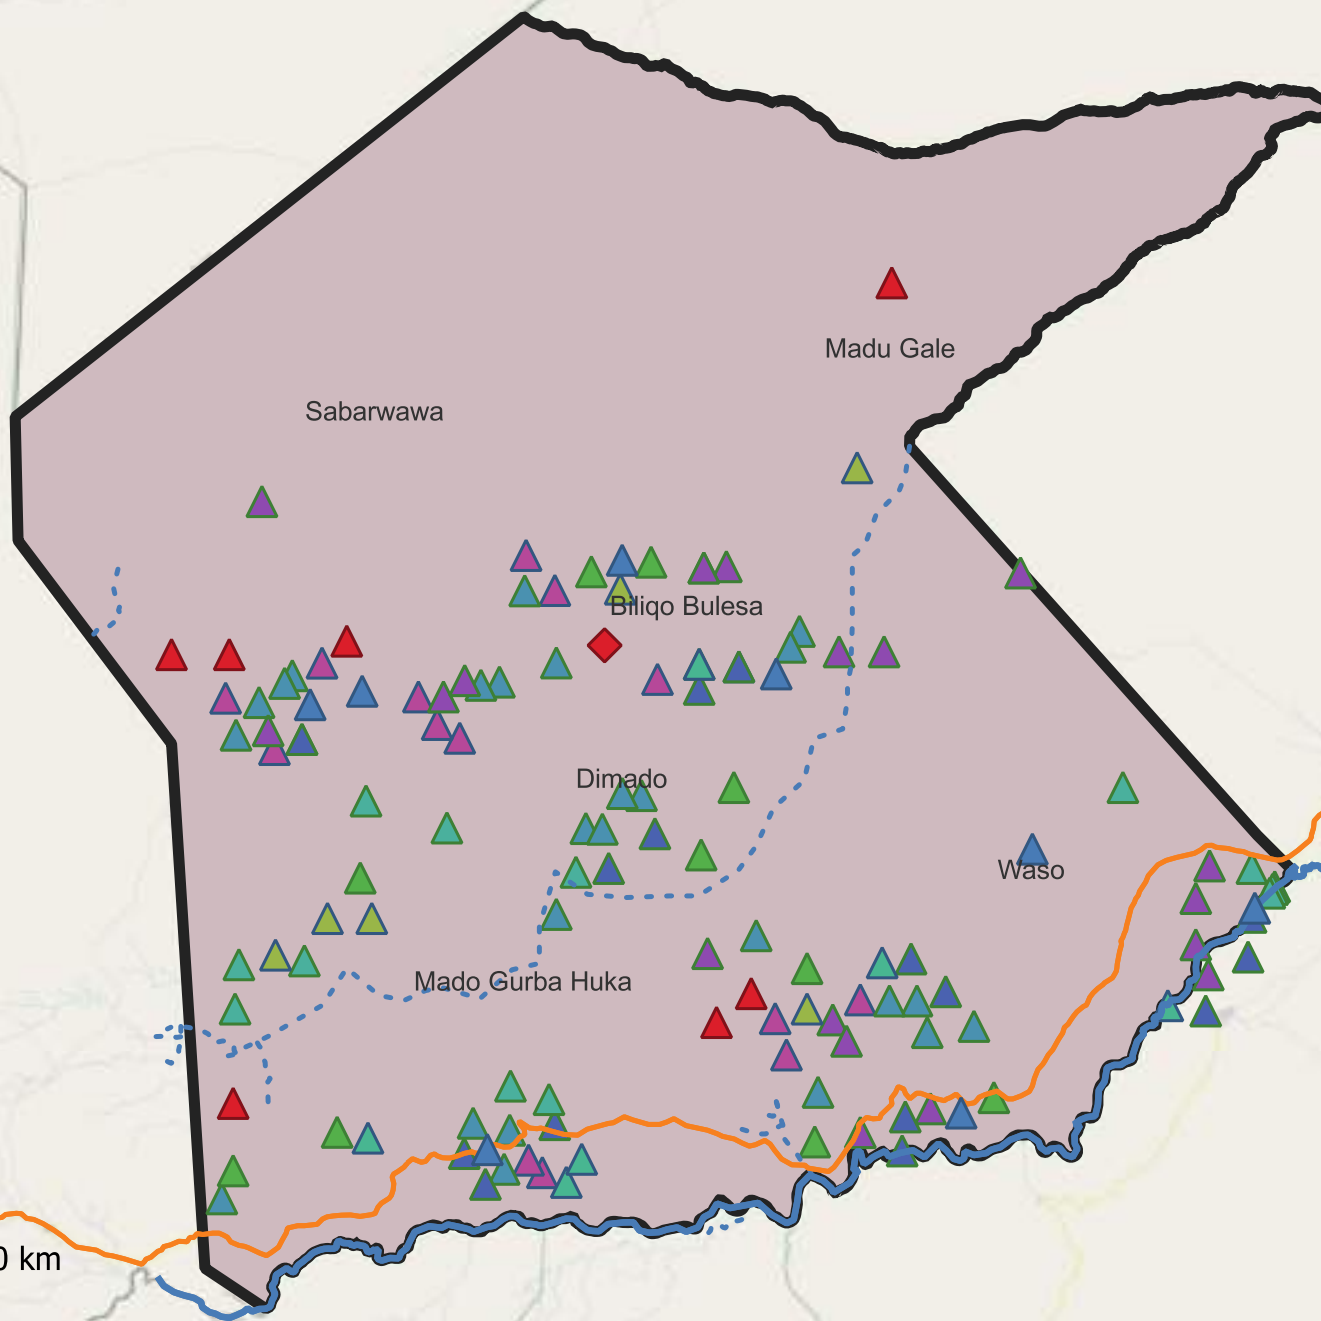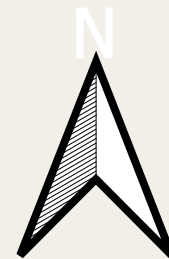

- Wild Dog
- Oryx
- Lion
- Lesser kudu
- Leopard
- Greffy Zebra
- Greater Kudu
- Giraffe
- Elephants
- Cheetah
- Conservancy HQ
- Biliqa-Bulesa Conservancy
- Road major
- River minor
- River

Leparua Community Conservancy



Nasulu Community Conservancy

Leparua
Community
Conservancy

ISIOLO

Lewa Wildlife Conservancy

LEGEND

- Road major
- River
- Road Minor
- Biliqa-Bulesa Conservancy
- Conservancy Block

0 4.5 9 km

Biliqa-Bulesa Conservancy

Marsabit

Samburu

Isiolo

0 25 km

Leparua Community Conservancy

Laikipia

Isiolo

Meru

0 2.5 5 km

Isiolo County

Marsabit

Wajir

Samburu

Isiolo

Narapicho Community Conservancy

Nasulu Community Conservancy

Laikipia

conservancy

ana Conservancy

Wildlife Conservancy

Meru

Garissa

Tharaka-Nithi

Nyeri


Kirinyaga

Embu

Kitui

0 100 km

- Road Minor
- Road major
- River
- Biliqa-Bulesa Conservancy
- Leparua Community Conservancy
- Isiolo County

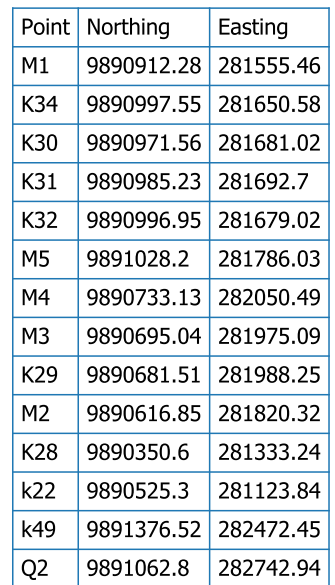



COMPILED BY: V. OUNDO SIGN: DATE:

APPROVED BY: F. ODUOR SIGN: DATE:

DATE: 28-07-2022

PROPOSED HOLA SUBSTATION

SCALE: 1:5,000

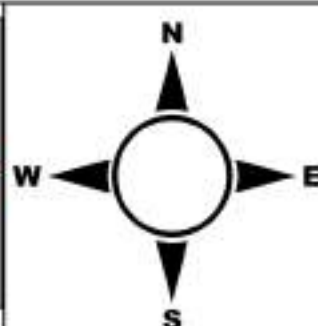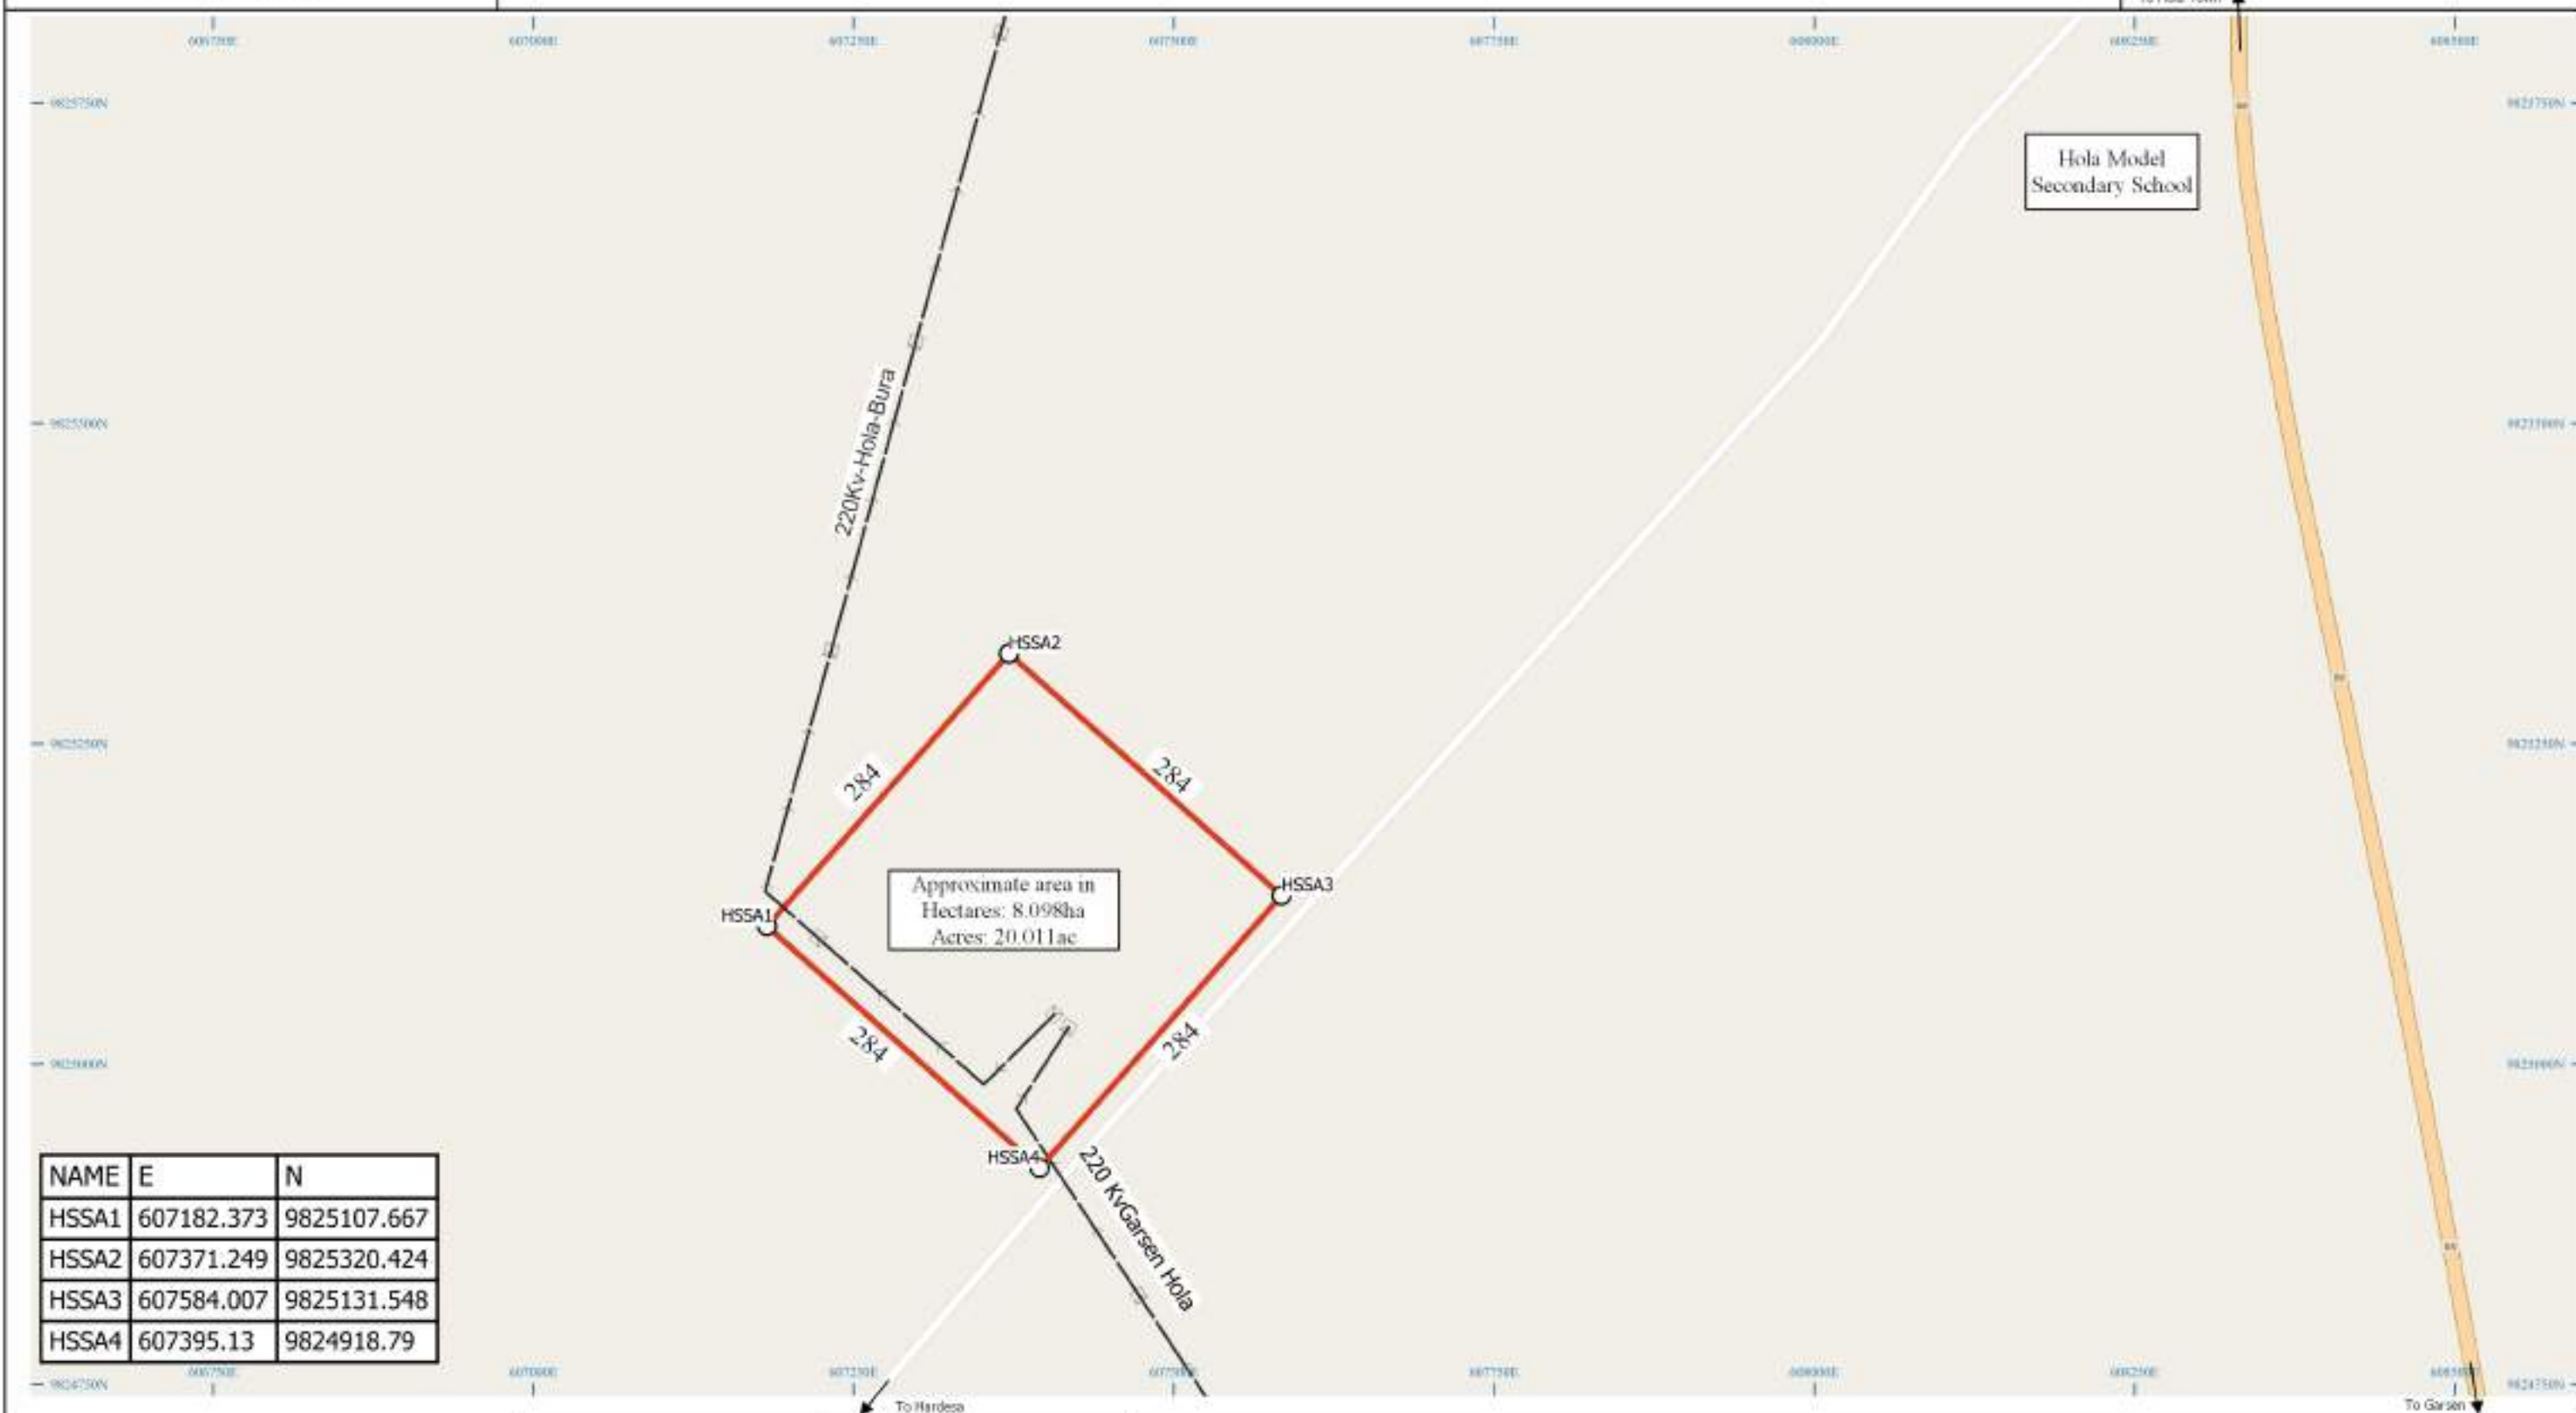

COORDINATE SYSTEM:

UTM Projection
Datum: Arc 1960
Zone 36
Southern Hemisphere
Units: Metres
EPSG: 21036

This map is not conclusive on the precise position on any boundaries unless this has been fixed in accordance with Sec. 22 of Registered Land Act.
The coordinates are obtained from georeferencing of PIDs and are for general identification of the parcels only.

Distances are approximate, subject to Final Survey

Drawn by Vincent Cheruiyot


Legend

- Corner Beacons
- Hola-substation


DATE: 28-07-2022

PROPOSED HOLA SUBSTATION

SCALE: 1:5,000

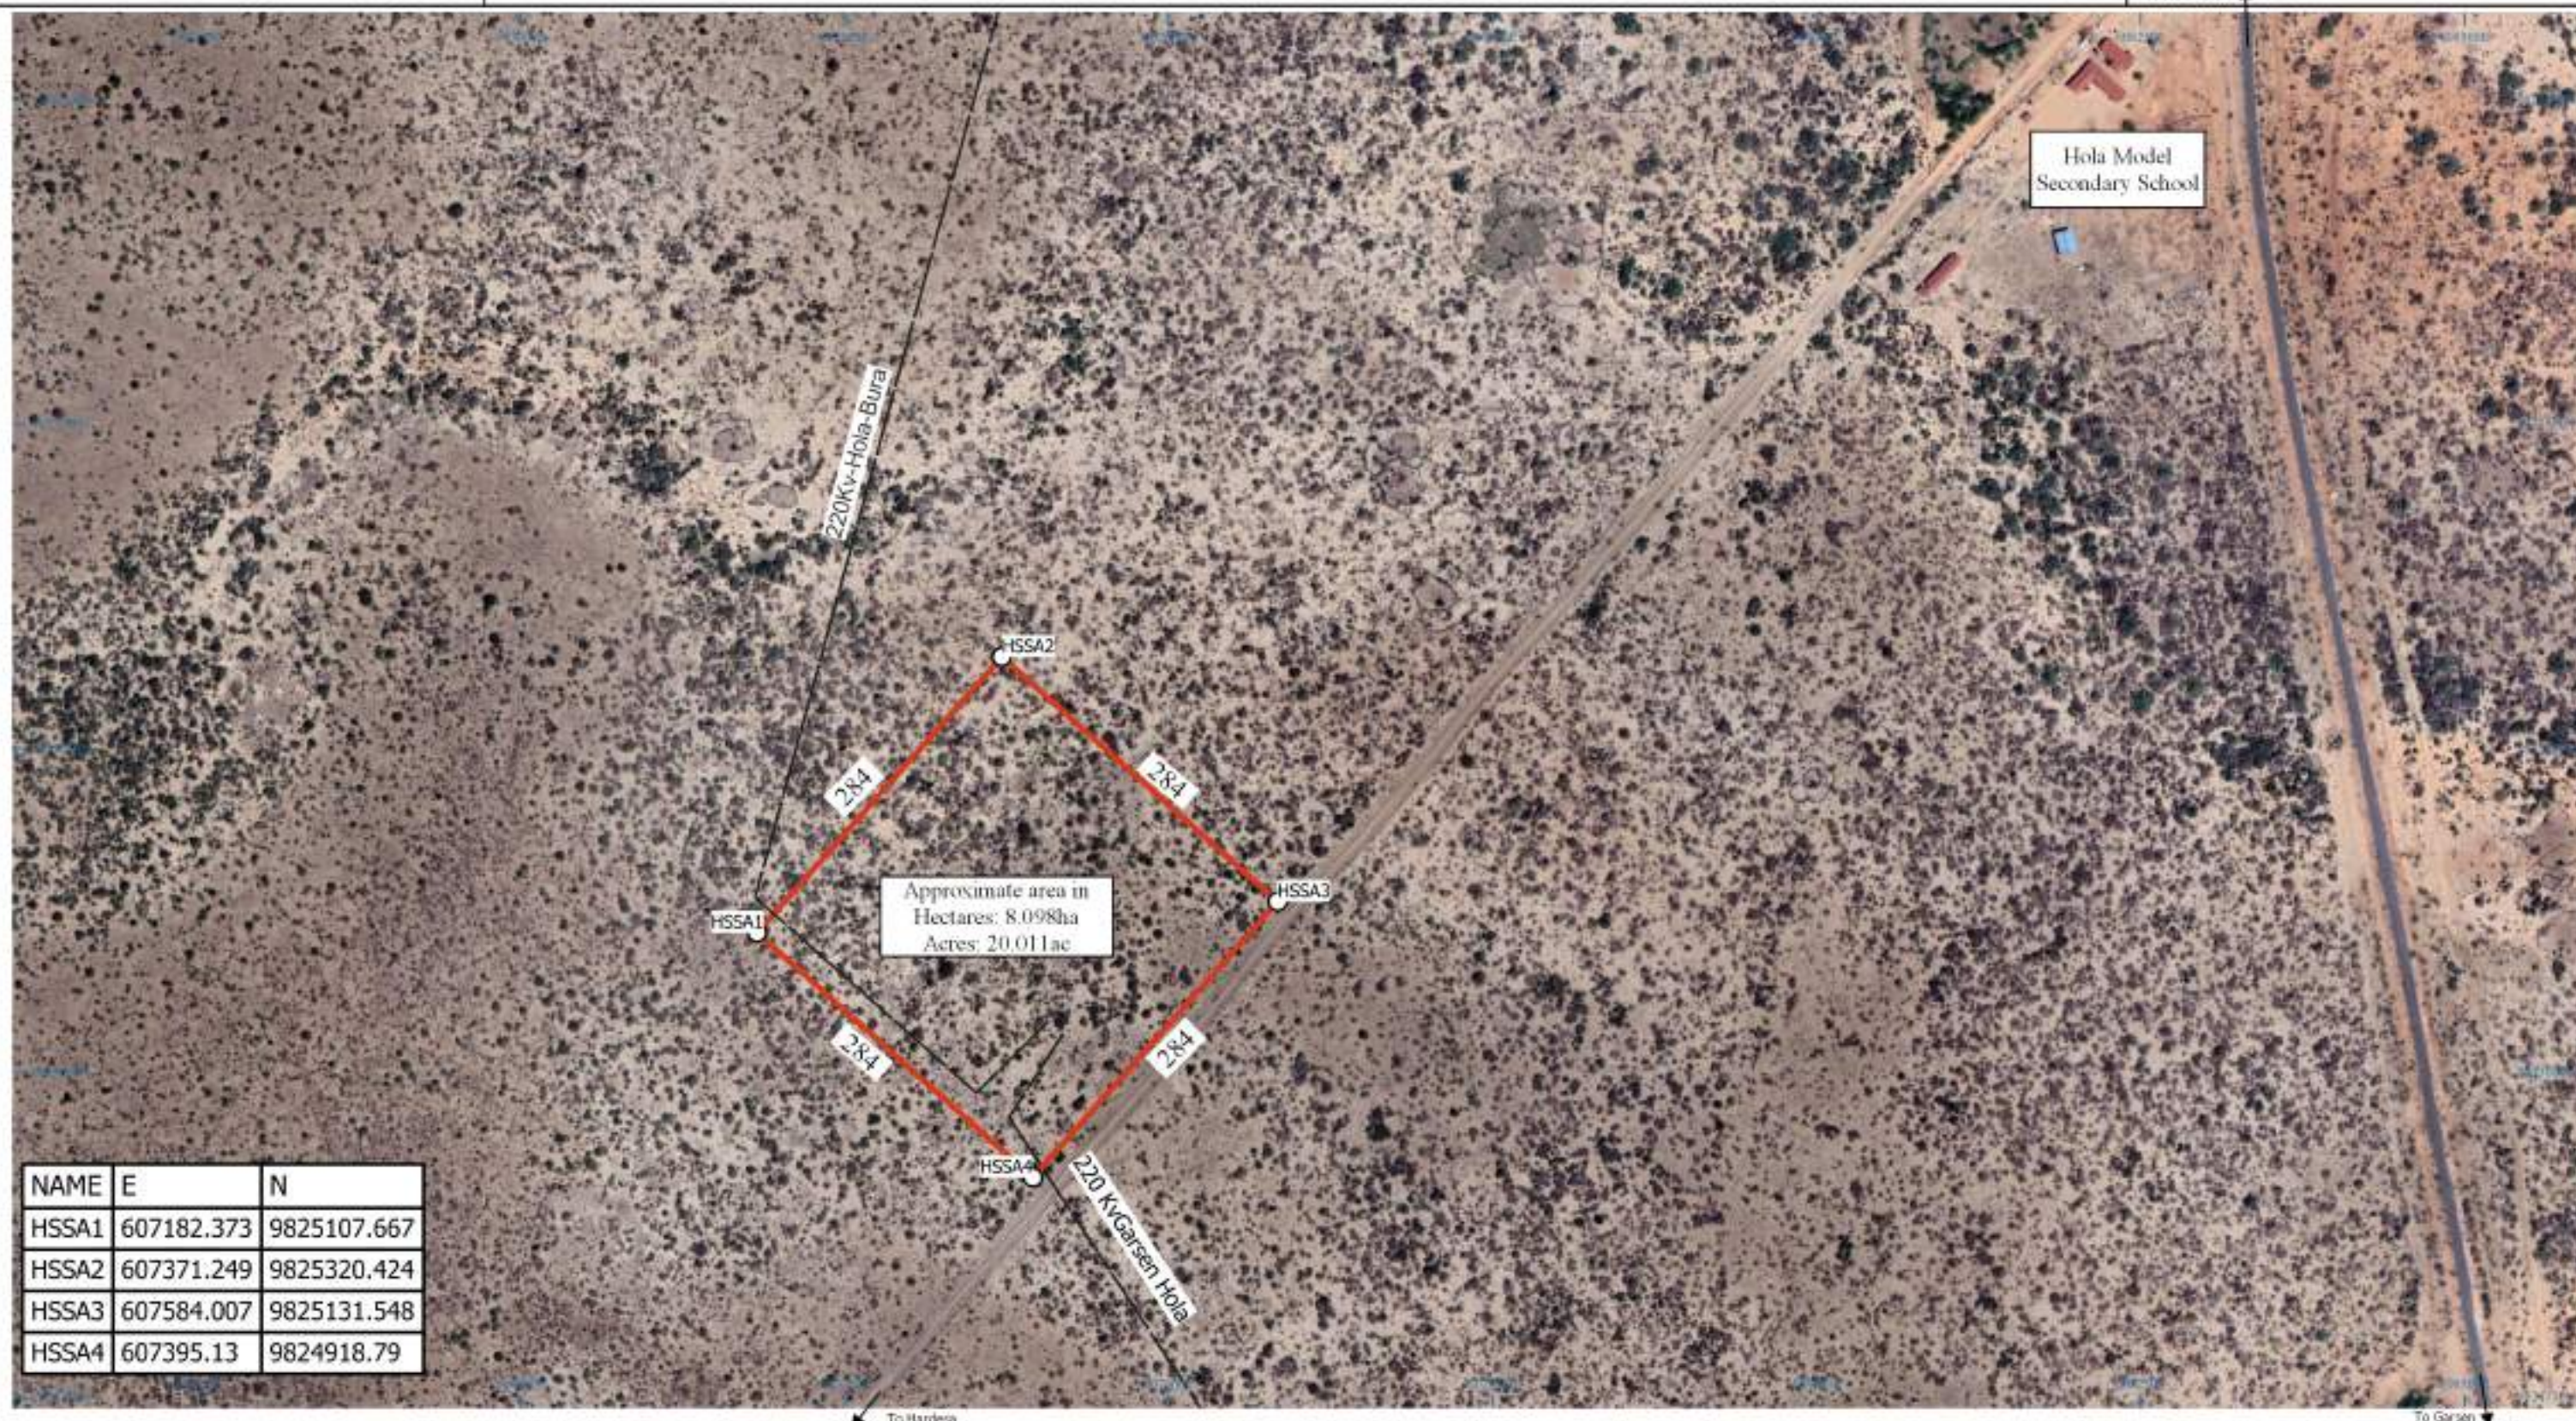

NAME	E	N
HSSA1	607182.373	9825107.667
HSSA2	607371.249	9825320.424
HSSA3	607584.007	9825131.548
HSSA4	607395.13	9824918.79

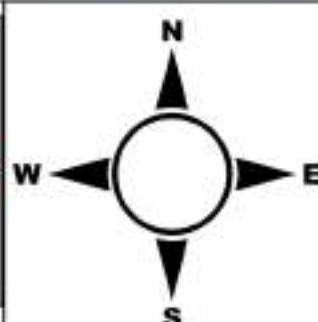

COORDINATE SYSTEM:

UTM Projection
Datum: Arc 1960
Zone 36
Southern Hemisphere
Units: Metres
EPSG: 21036

This map is not conclusive on the precise position on any boundaries unless this has been fixed in accordance with Sec. 22 of Registered Land Act.
The coordinates are obtained from georeferencing of PIDs and are for general identification of the parcels only.

Distances are approximate, subject to Final Survey

Drawn by Vincent Cheruiyot

Legend

- Corner Beacons
- Hola-substation


DATE: 28-07-2022

PROPOSED BURA SUBSTATION

SCALE: 1:5,000



Name	E.	N.
BSS1	587810	9873474
BSS2	588095	9873465
MJ2	588089	9873277
MJ3	587805	9873286

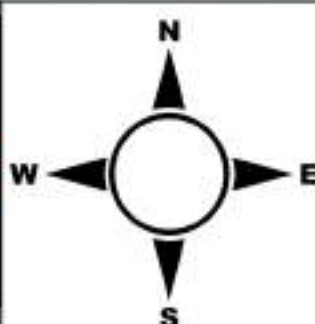

COORDINATE SYSTEM

UTM Projection
Datum: Arc 1960
Zone 36
Southern Hemisphere
Units: Metres
EPSG: 21036

This map is not conclusive on the precise position on any boundaries unless this has been fixed in accordance with Sec. 22 of Registered Land Act.

The coordinates are obtained from georeferencing of PIDs and are for general identification of the parcels only.

Distances are approximate, subject to Final Survey

Drawn by Vincent Cheruiyot


Legend

- Corner Beacons
- Bura Substation


DATE: 28-07-2022

PROPOSED BURA SUBSTATION

SCALE: 1:5,000

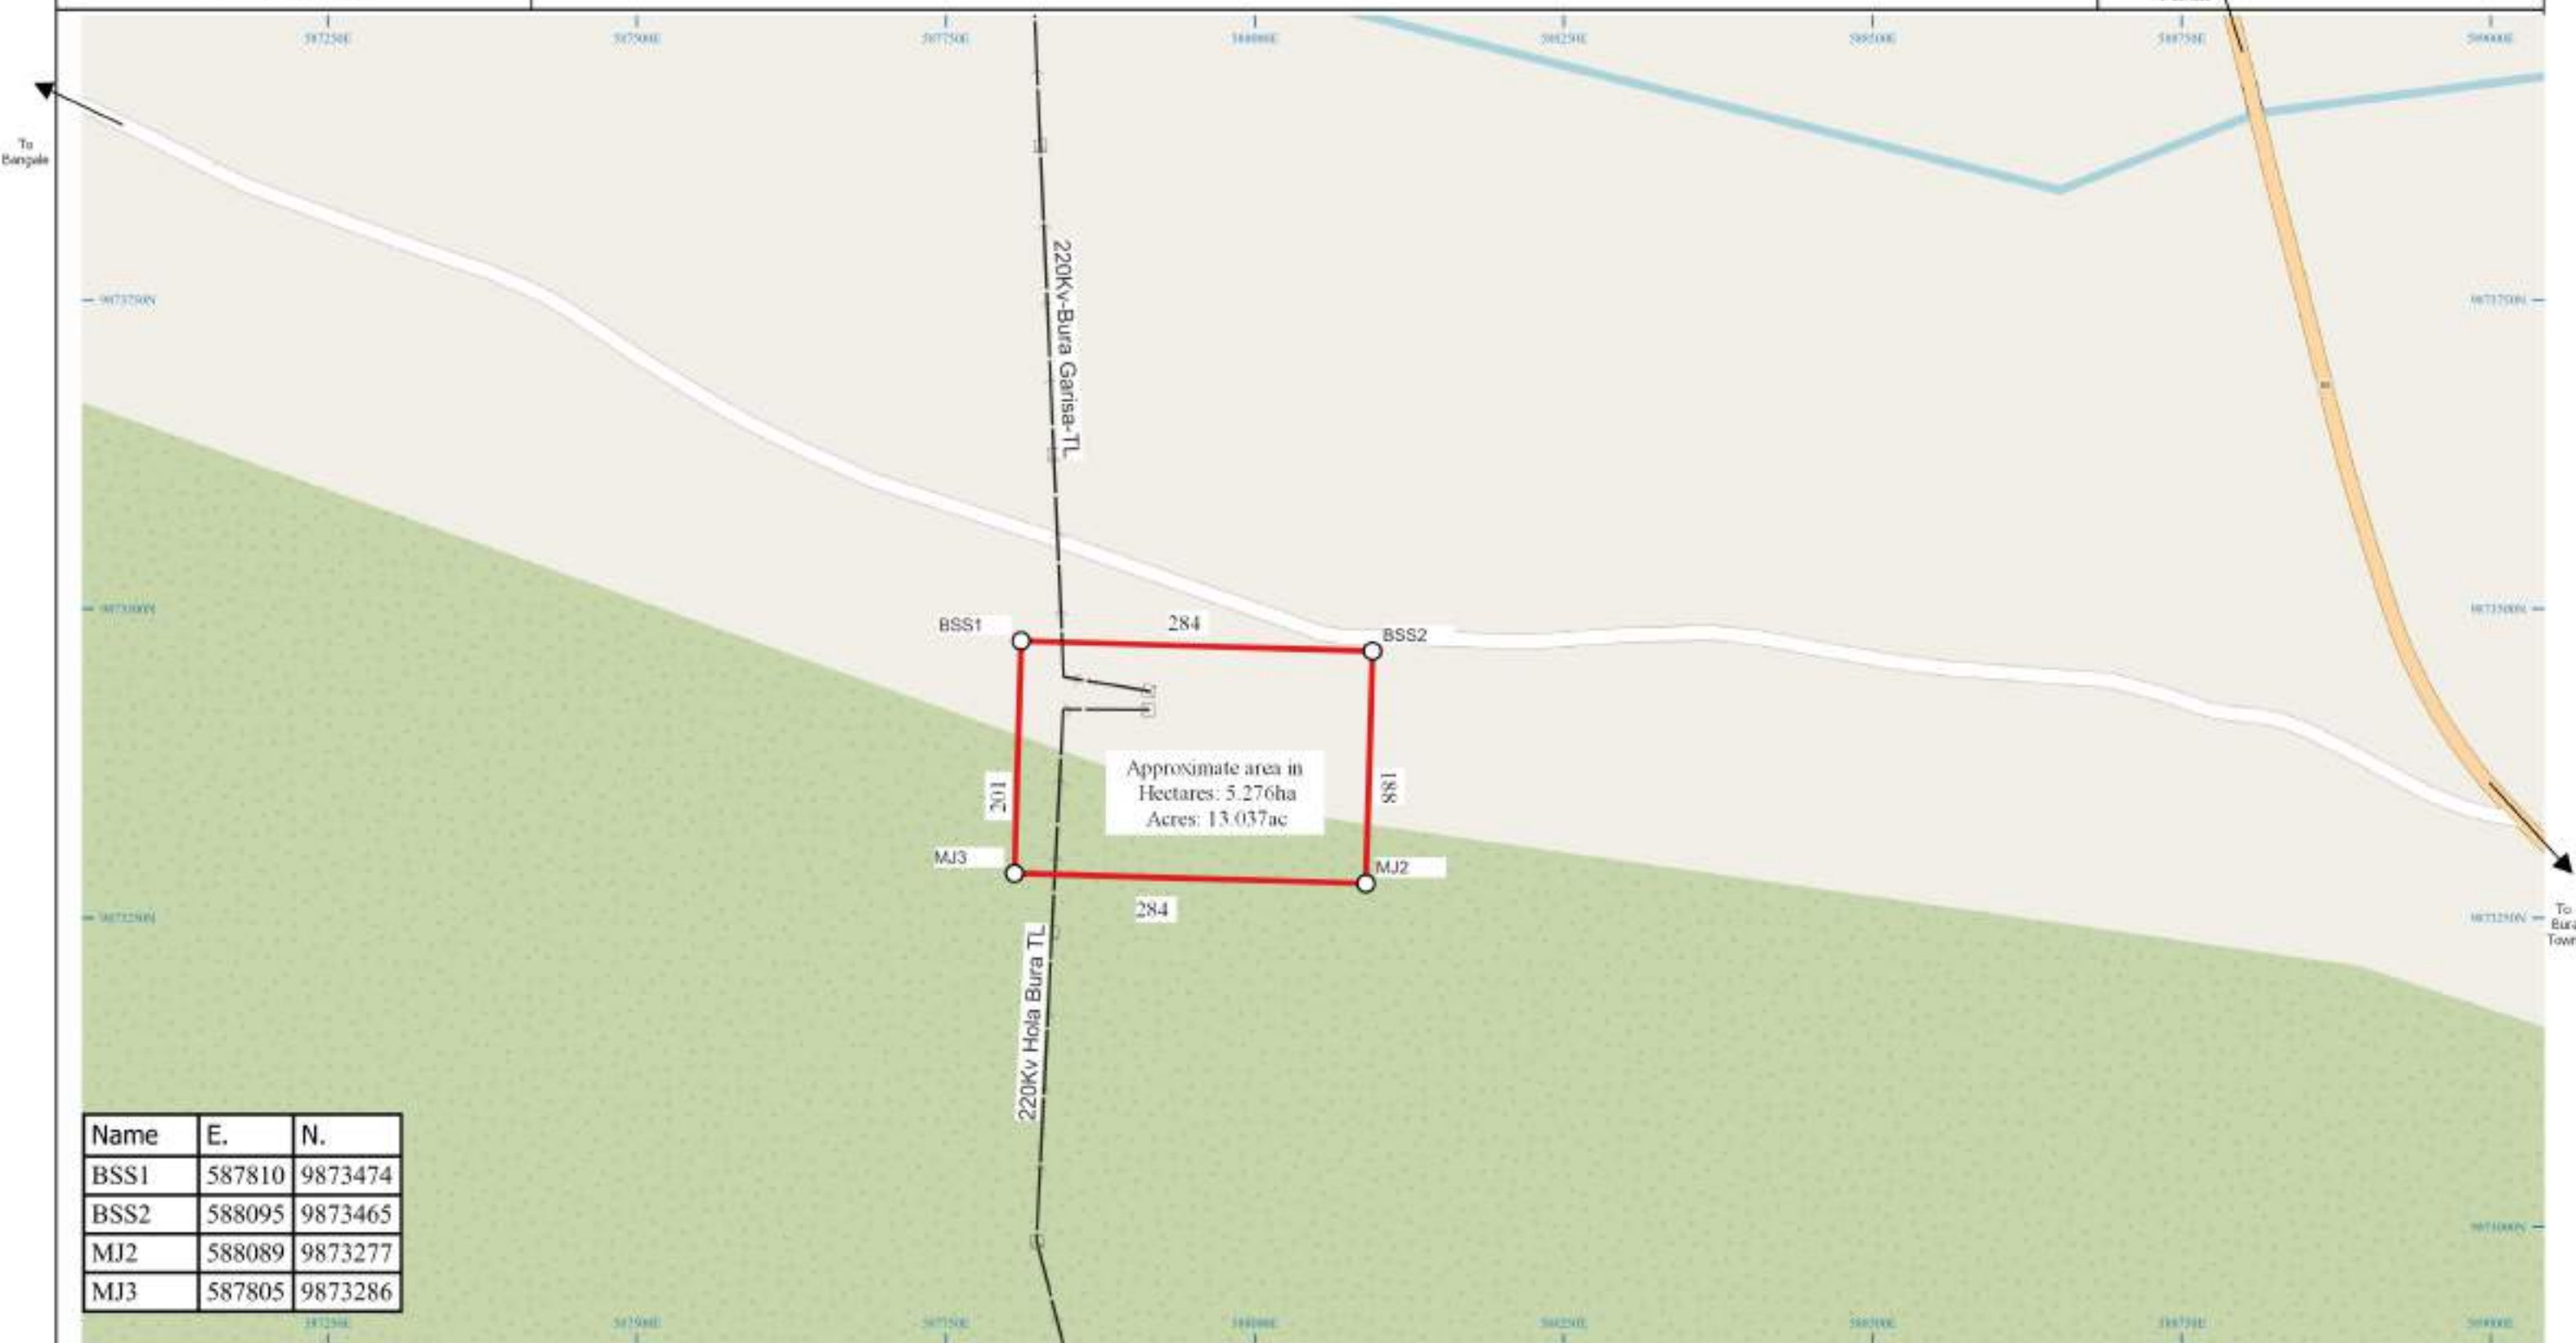

Name	E.	N.
BSS1	587810	9873474
BSS2	588095	9873465
MJ2	588089	9873277
MJ3	587805	9873286

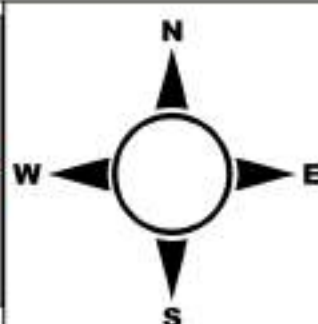

COORDINATE SYSTEM

UTM Projection
Datum: Arc 1960
Zone 36
Southern Hemisphere
Units: Metres
EPSG: 21036

This map is not conclusive on the precise position on any boundaries unless this has been fixed in accordance with Sec. 22 of Registered Land Act.

The coordinates are obtained from georeferencing of PIDs and are for general identification of the parcels only.

Distances are approximate, subject to Final Survey


Drawn by Vincent Cheruiyot


Legend

- Corner Beacons
- Bura Substation


PROPOSED BURA SUBSTATION



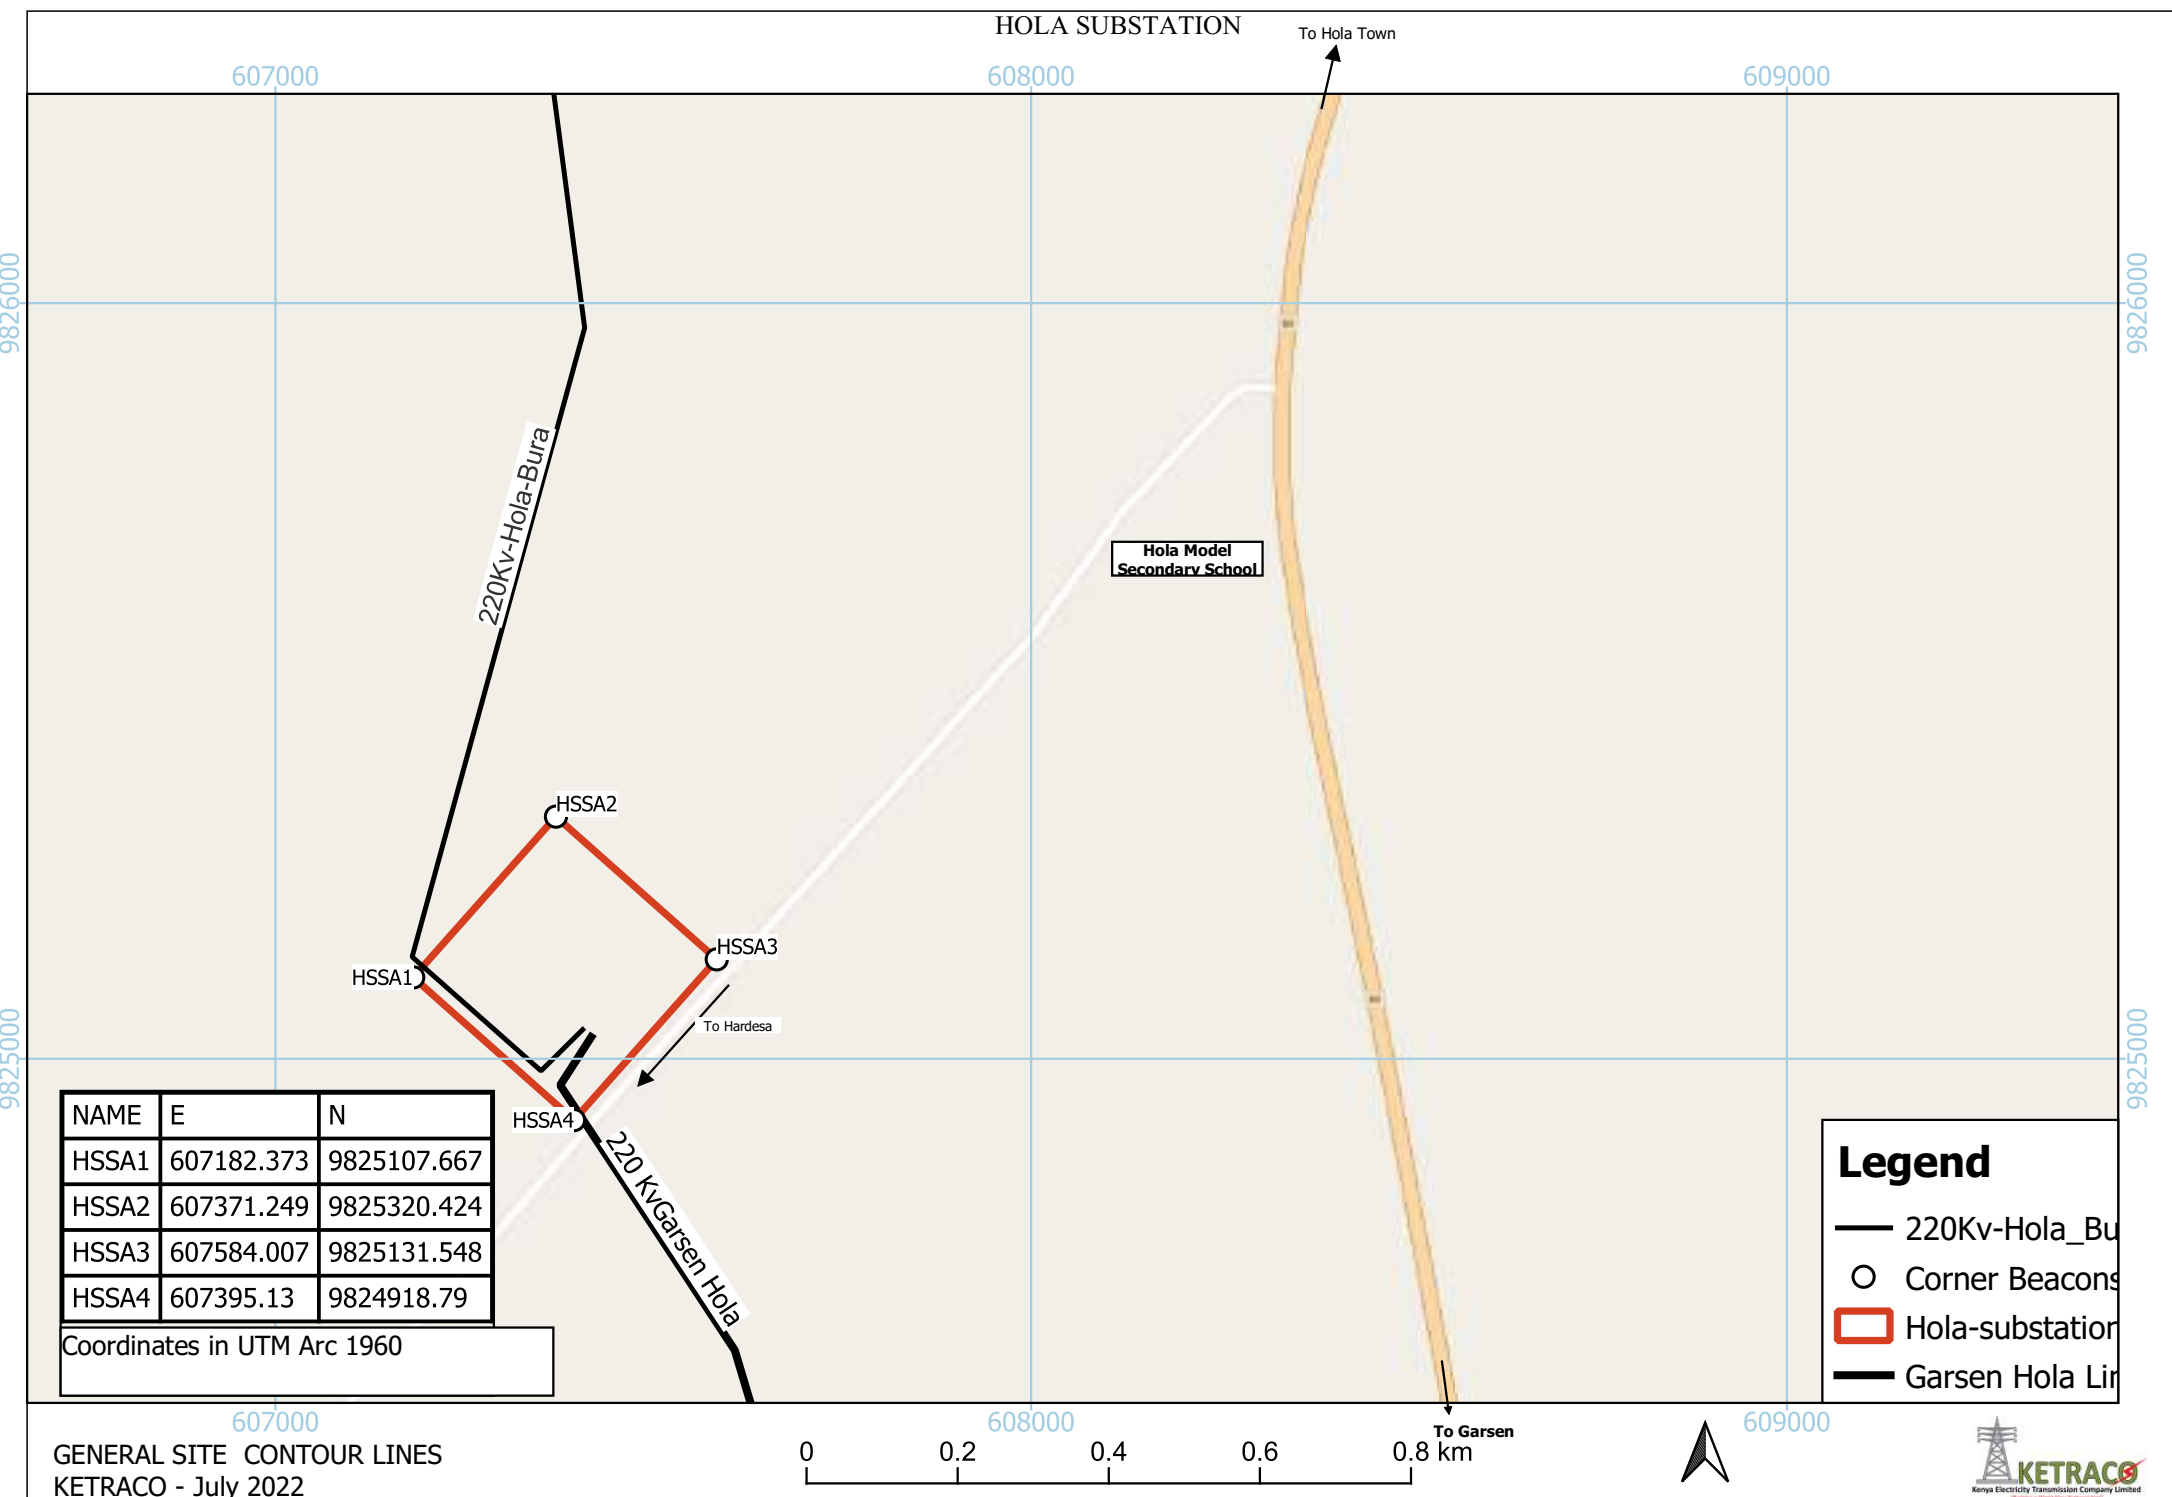

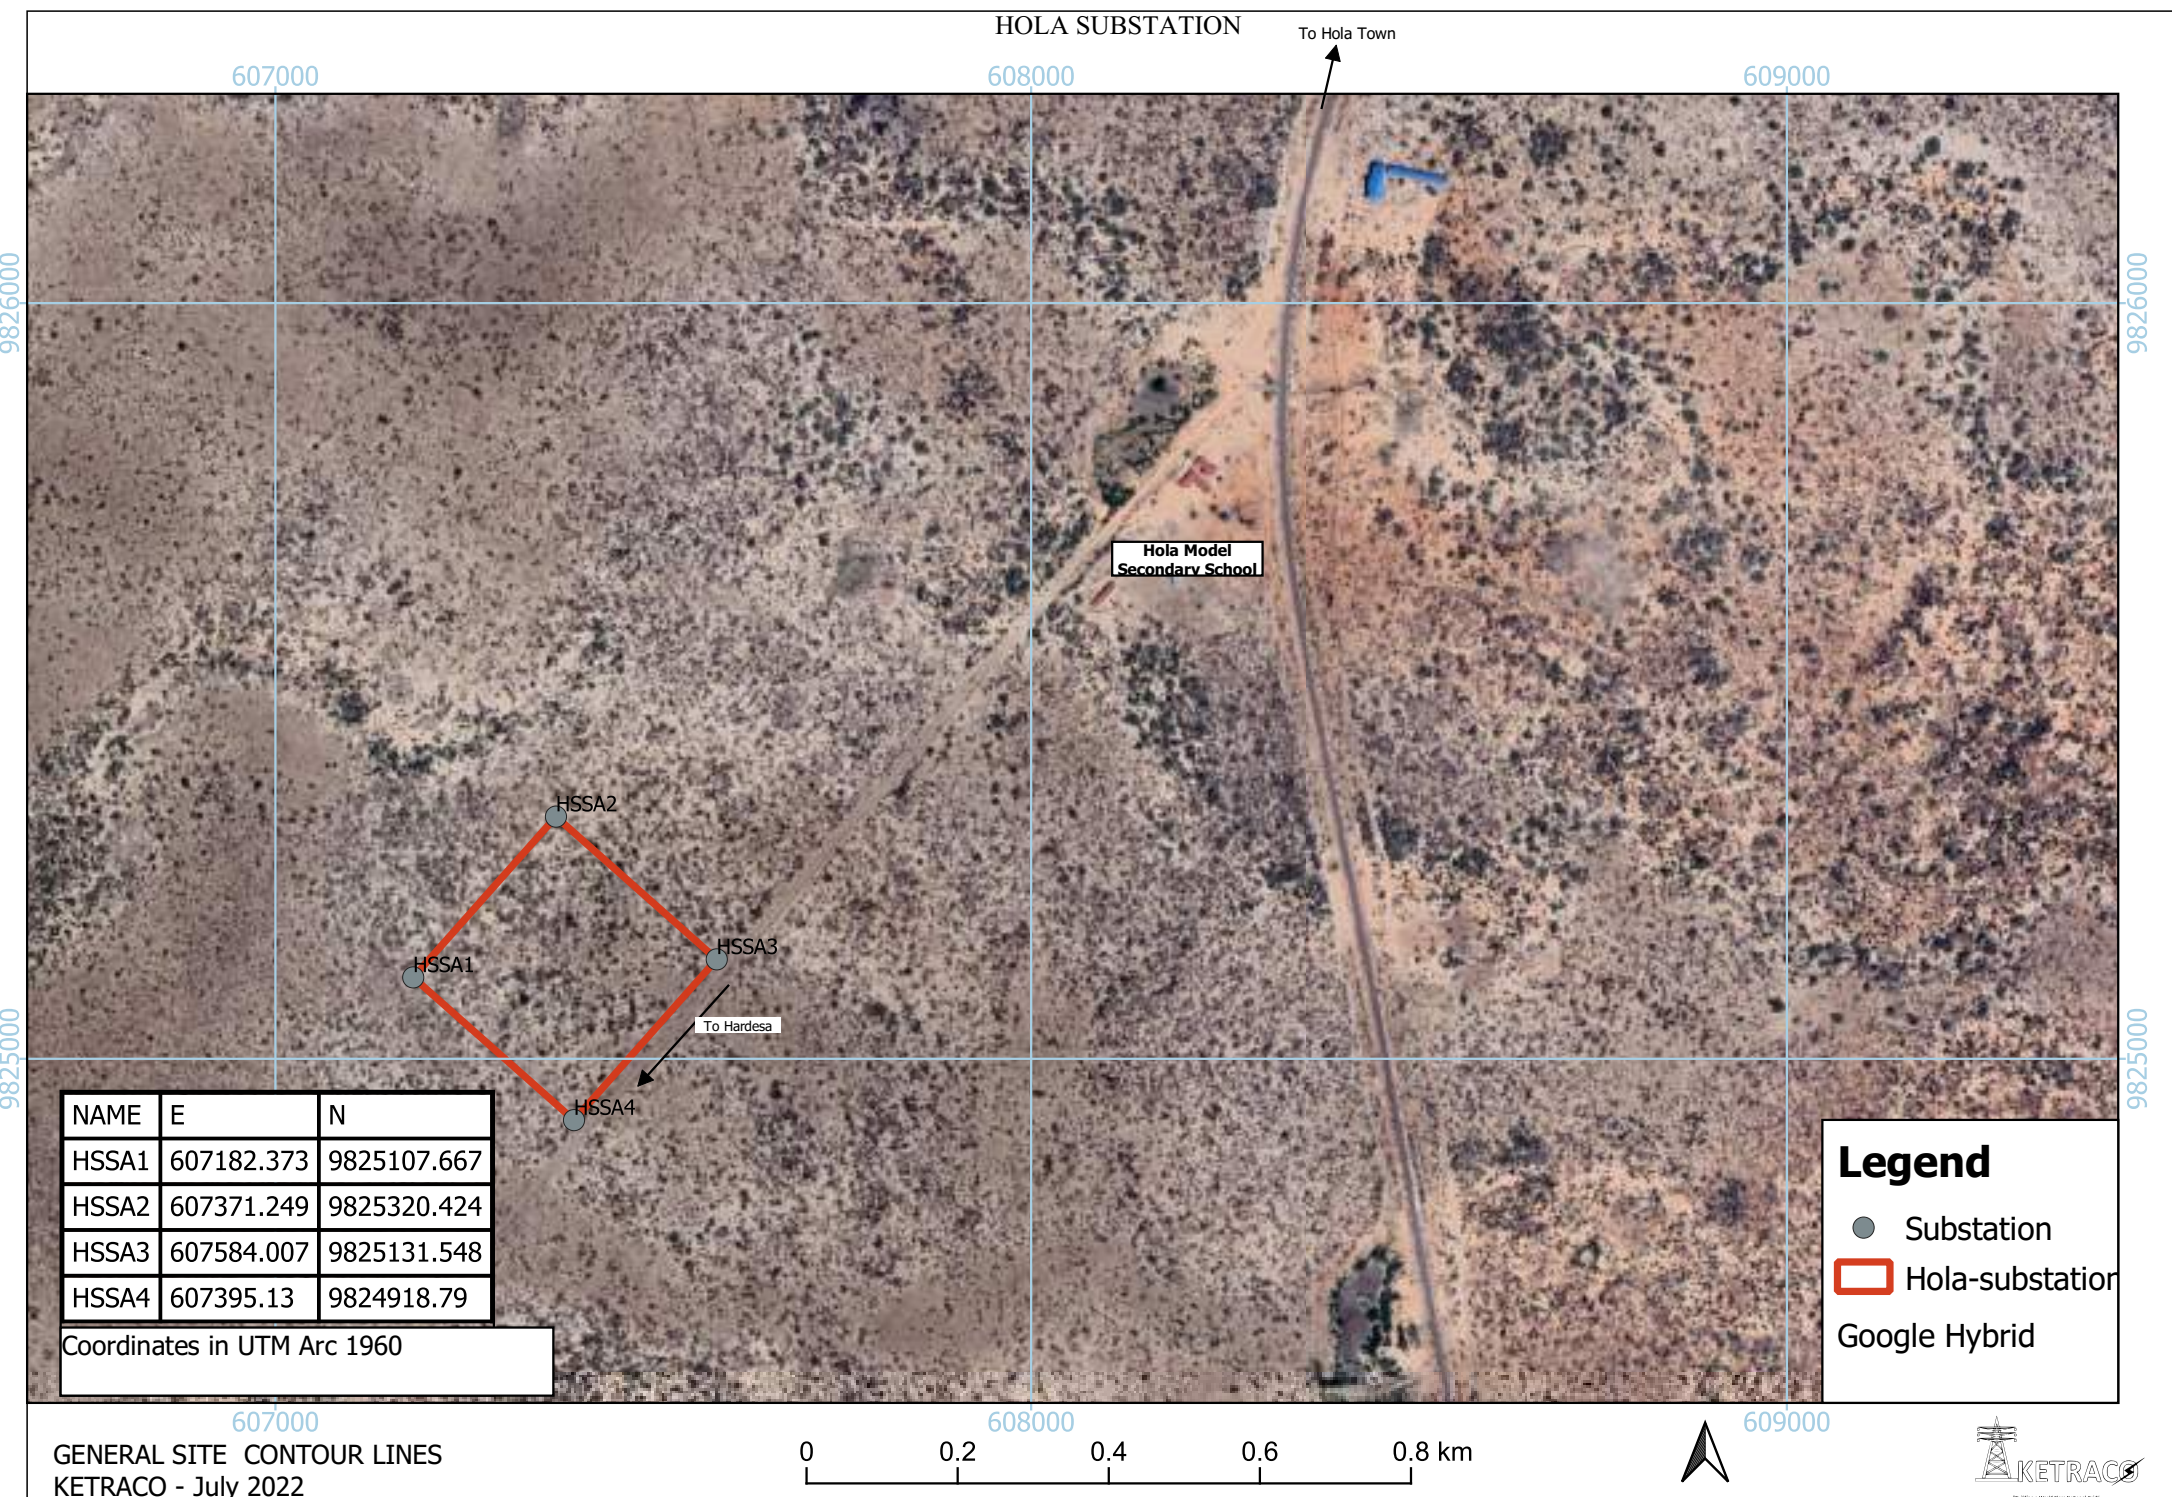

NAROK BOMET

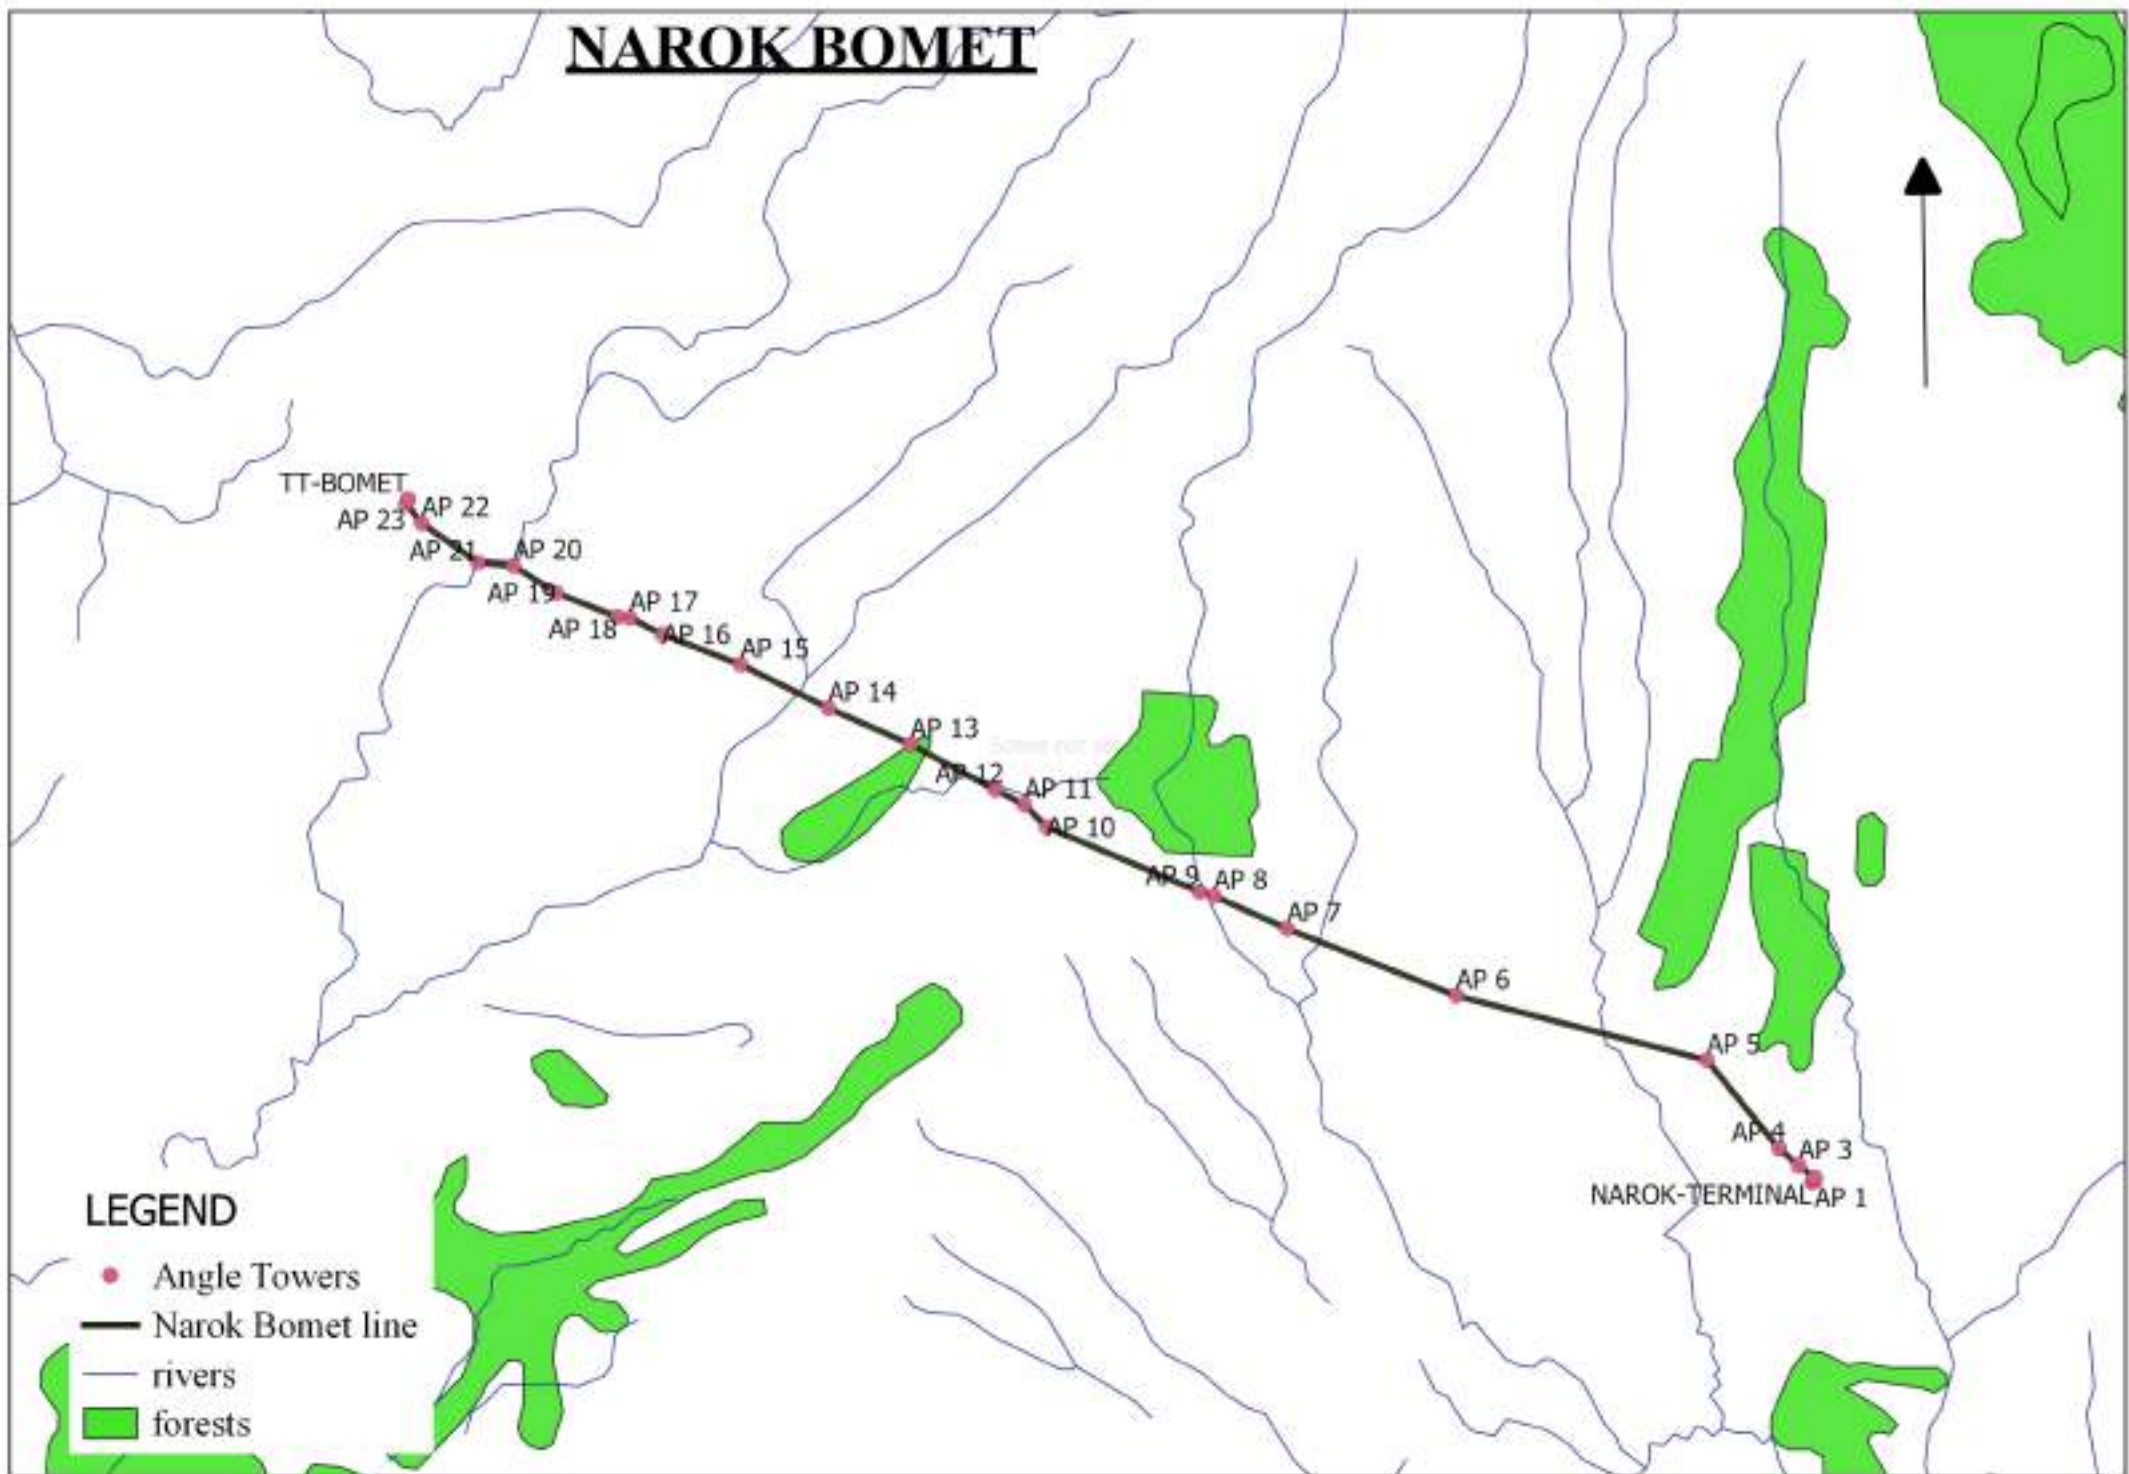



NANYUKI-ISIOLO-MERU 132KV T.L

LR NO 6875/2 AND LR NO 6875/3

MARCH 2022

SHEET 19

EASTINGS	NORTHINGS	POINT
293815	7558	18
291054	7558	M
290629	6925	11
291474	5774	A
292656	6701	C
292005	6238	AIC
291000	6353	AX M
292186	7274	BX
291864	6485	DX
291169	5943	EX
291953	7558	DN

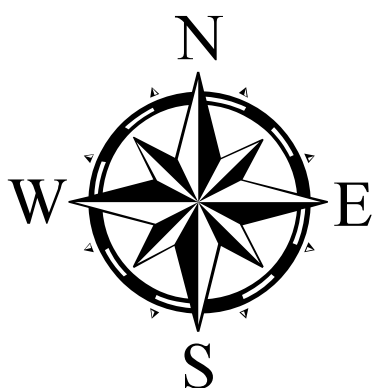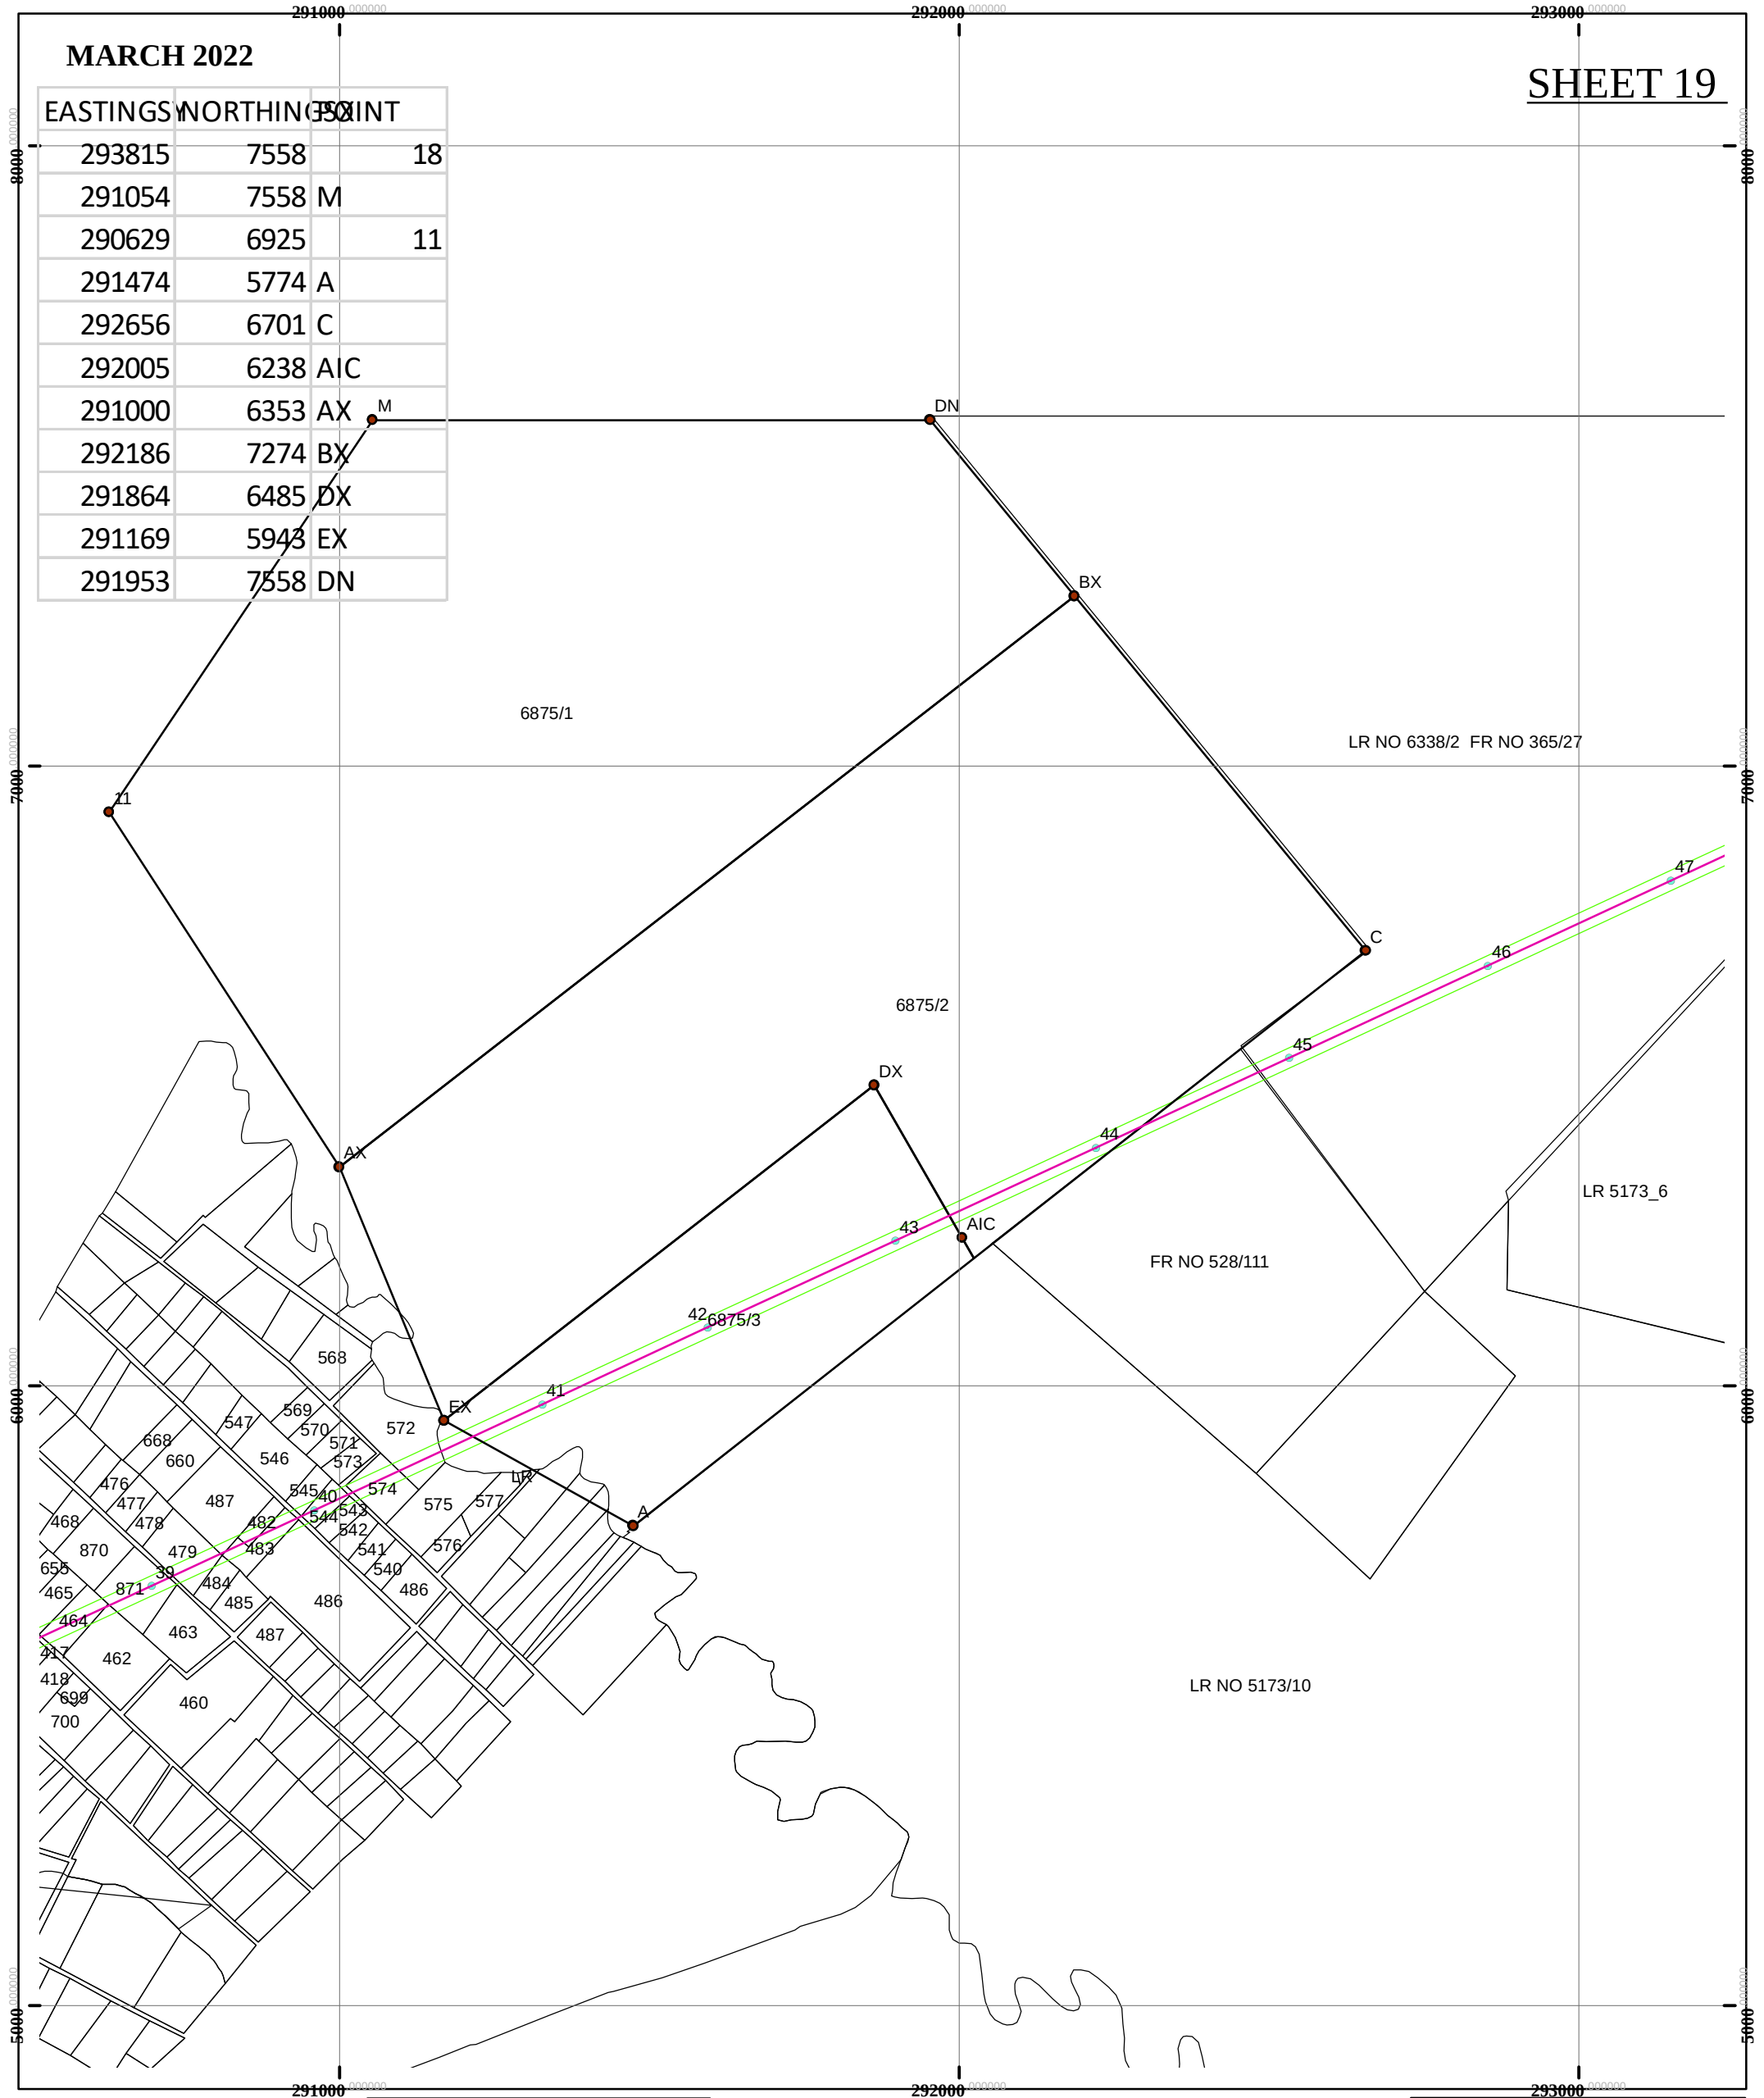

**THE UTM COORDINATES
HAVE BEEN DERIVED FROM
CASSINI COORDINATES IN
FR 45_187**

Legend

- | | |
|---|----------------------------------|
|  | LR 6875_2 & 3 FR 45_187 |
|  | NIM_30M_CL_Jan_2022 |
|  | NIM_30M_BUFFER_Jan_2022 |
|  | NIM_30M_TOWERS_JAN_2022 |
|  | LAI DAIGA UMANDE BLK 6 NYARIGINU |
|  | LR_NOS |


GRID :UTM ZONE 37N
DATUM :ARC 1960
UNITS :METERS
SCALE : 1:10,000

Compiled By:D.K.Muthua

Checked By: F. Oduor FISK

NANYUKI-ISIOLO-MERU 132KV T.L


NANYUKI SOUTH TIMAU BLOCK 1 (NGENIA)/432

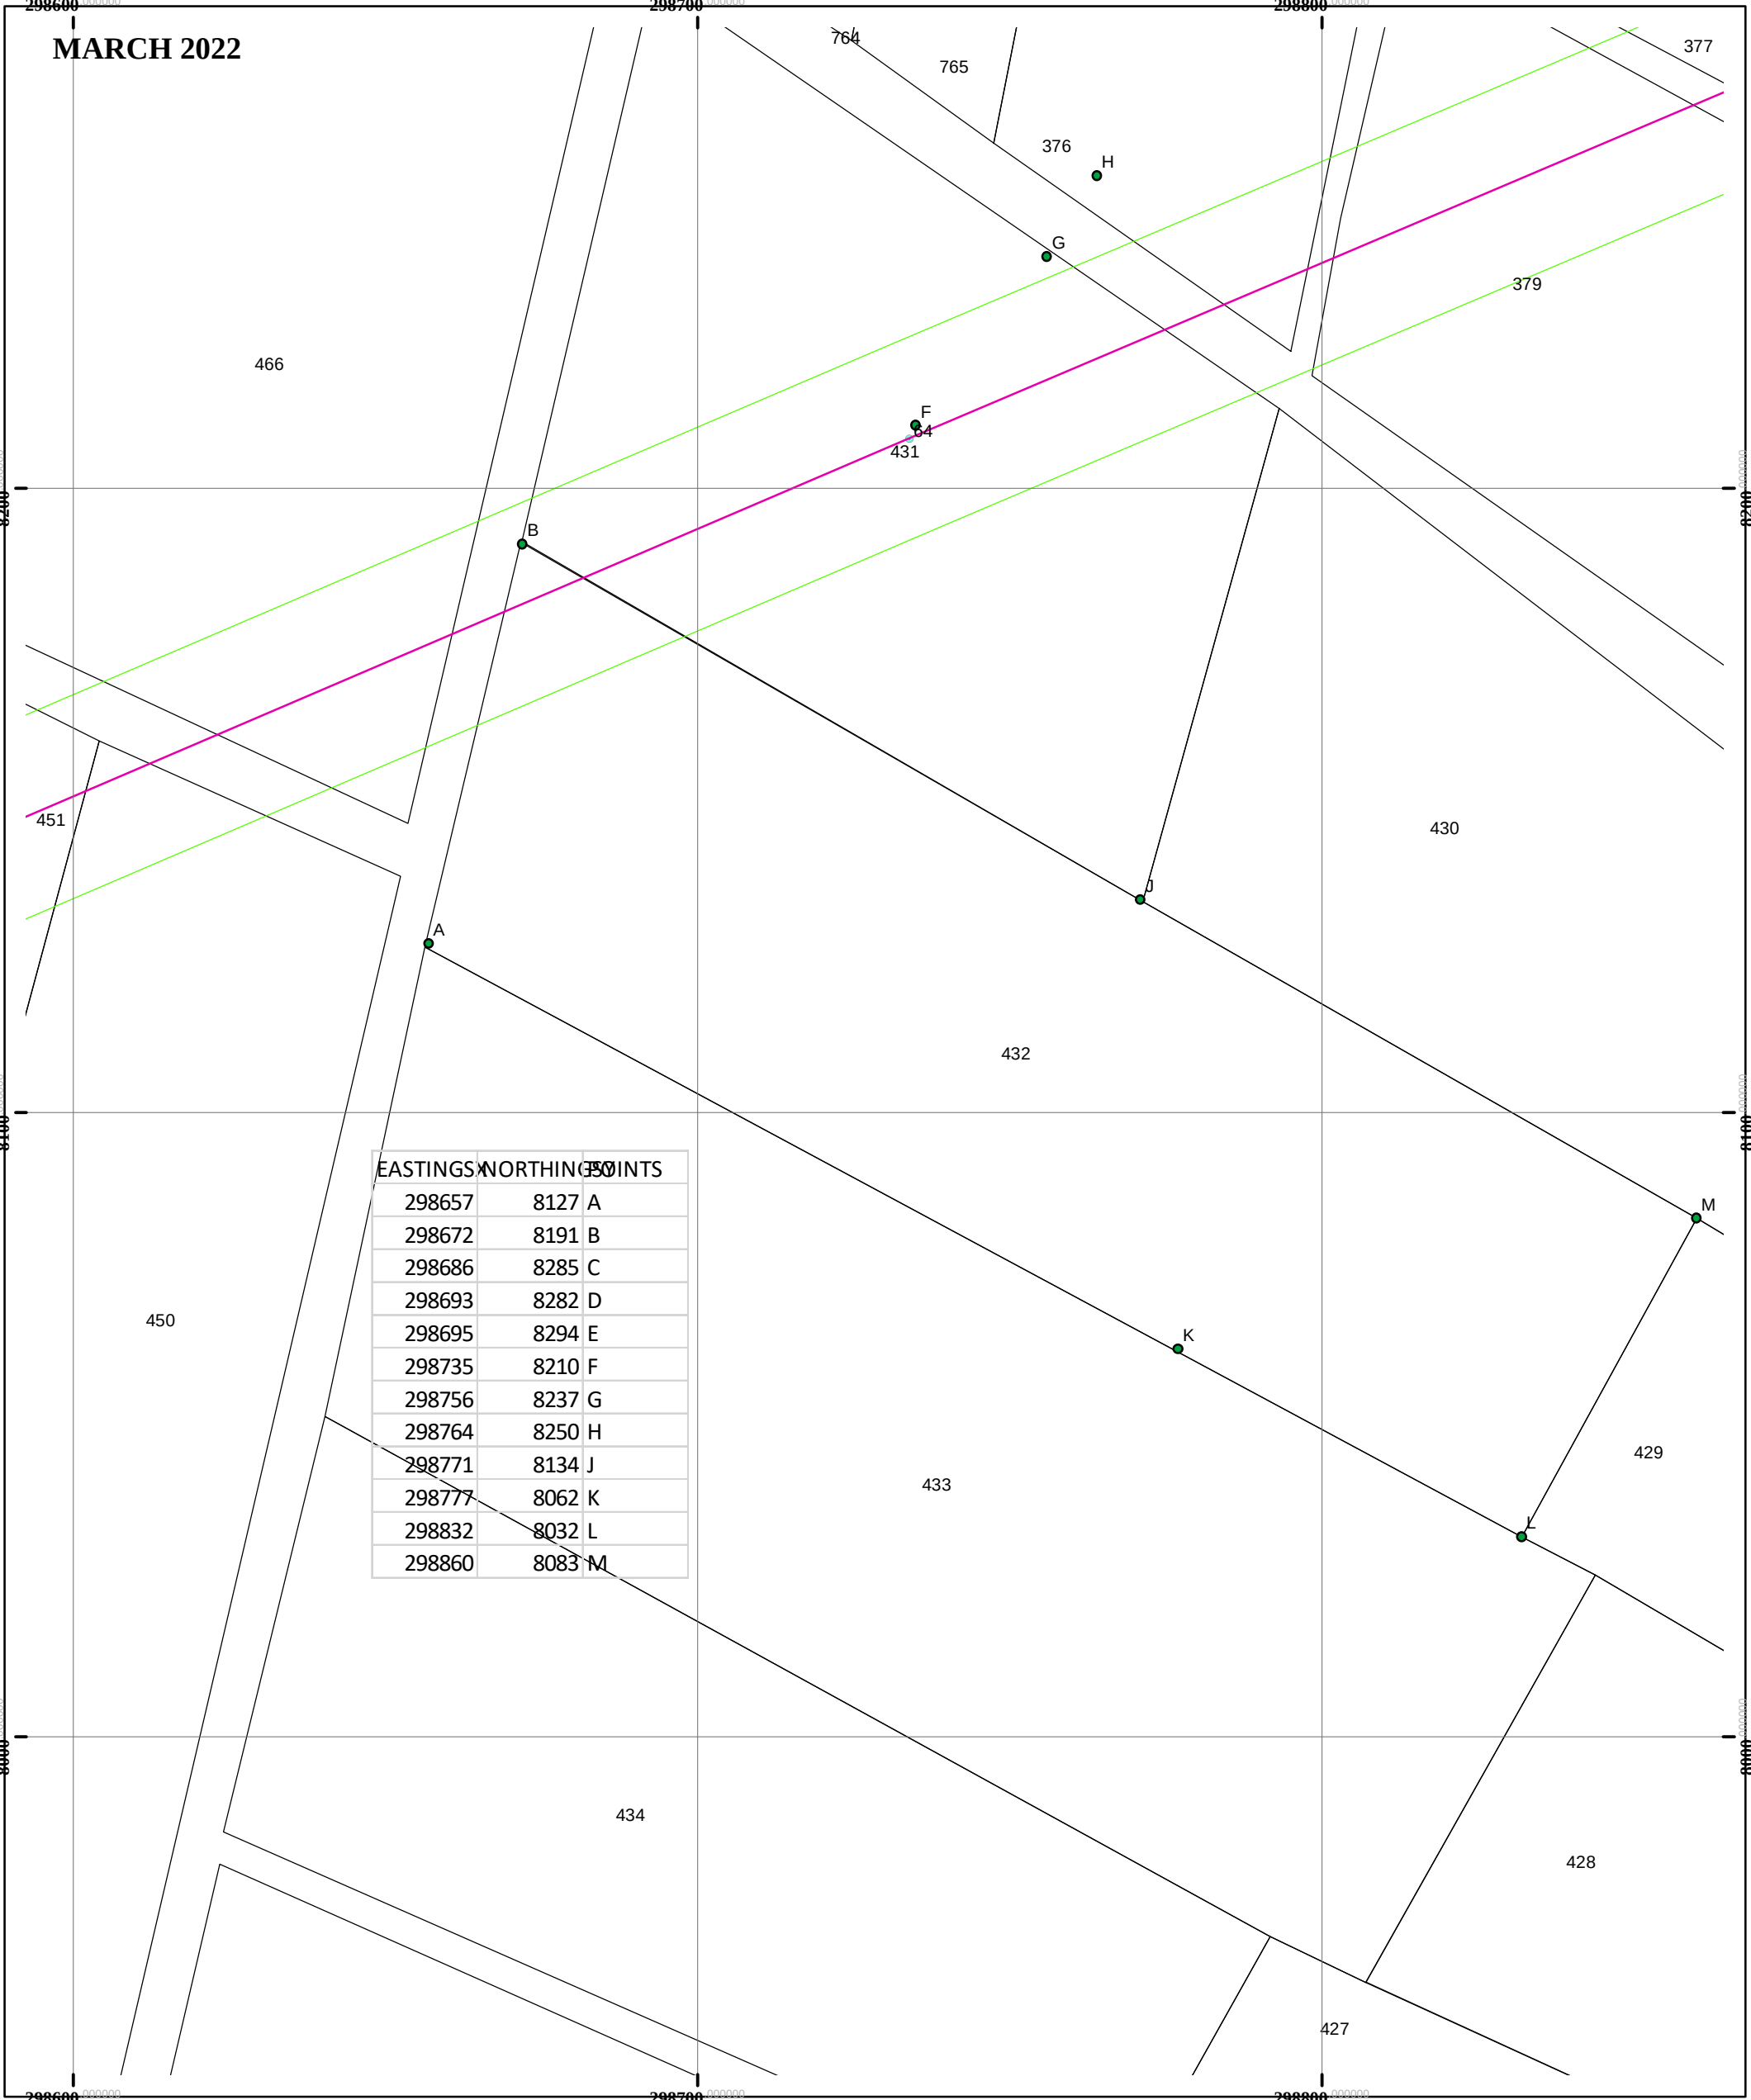



KETRACO
Building a World Class National Grid

**KENYA ELECTRICITY
TRANSMISSION COMPANY
LIMITED**

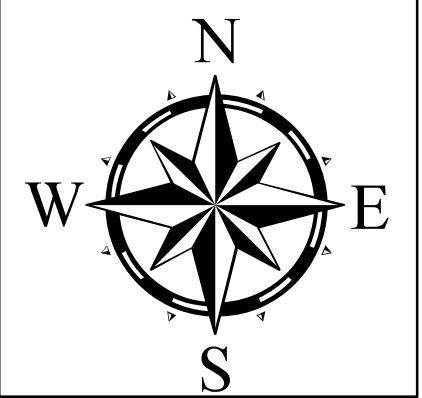

DISCLAIMER:
This map is not conclusive
on the precise position of
any boundary unless this
has been fixed in accordance
with Sec.19 of LRA.

Legend

- NGENIA 432
- NIM_30M_CL_Jan_2022
- NIM_30M_BUFFER_Jan_2022
- NIM_30M_TOWERS_JAN_2022
- NANYUKI-SOUTH TIMAU_NGENIA

GRID :UTM ZONE 37N
DATUM :ARC 1960
UNITS :METERS
SCALE : 1:1,000

Compiled By:D.K.Muthua
.....

Checked By:F.Oduor FISK
.....